
GEP Darstellungsmodell für Publikationsmodell IPW

Inhaltsverzeichnis

- Werkkataster Ist (Polygon, Linie, Punkt 1, Punkt 2)
- Teileinzugsgebiete Ist
- Teileinzugsgebiete Soll
- Massnahmenplan
- ALR
- Zustandsplan Kanalisation (Polygon, Linie, Punkt)
- Konfliktplan Schutzzonen
- Erschliessungsplan (Polygon, Linie 1, Linie 2, Punkt 1, Punkt 2)

Legende

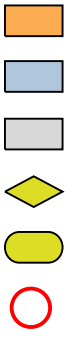

Darstellung

Klasse

Abfrage(n)

Stil-IDs Geometrie PAA + SAA

Stil-IDs Text

noch zu klärende Zuordnungen (siehe dazu auch Darstellungskatalog)

Filterkriterien

TEXT Attribut

TEXT Funktion

TEXT Wert

Darstellungsreihenfolge

TEXT Position (1 unten, 2 und höher überlagernd)


Version 0.8.3
Bearbeitung: Judith Germann, Carla Thoma
Freigabe: Jürg Lüthy
Bearbeitung für Publikationsmodell: Stefan Henrich, moflex Infra GmbH

GEP Darstellungsmodell für Publikationsmodell

Werkkataster Ist – Polygon

Bearbeitung: Judith Germann, Carla Thoma
Freigabe: Jürg Lüthy
Bearbeitung für Publikationsmodell: Stefan Henrich, moflex Infra GmbH

Version 0.8.3

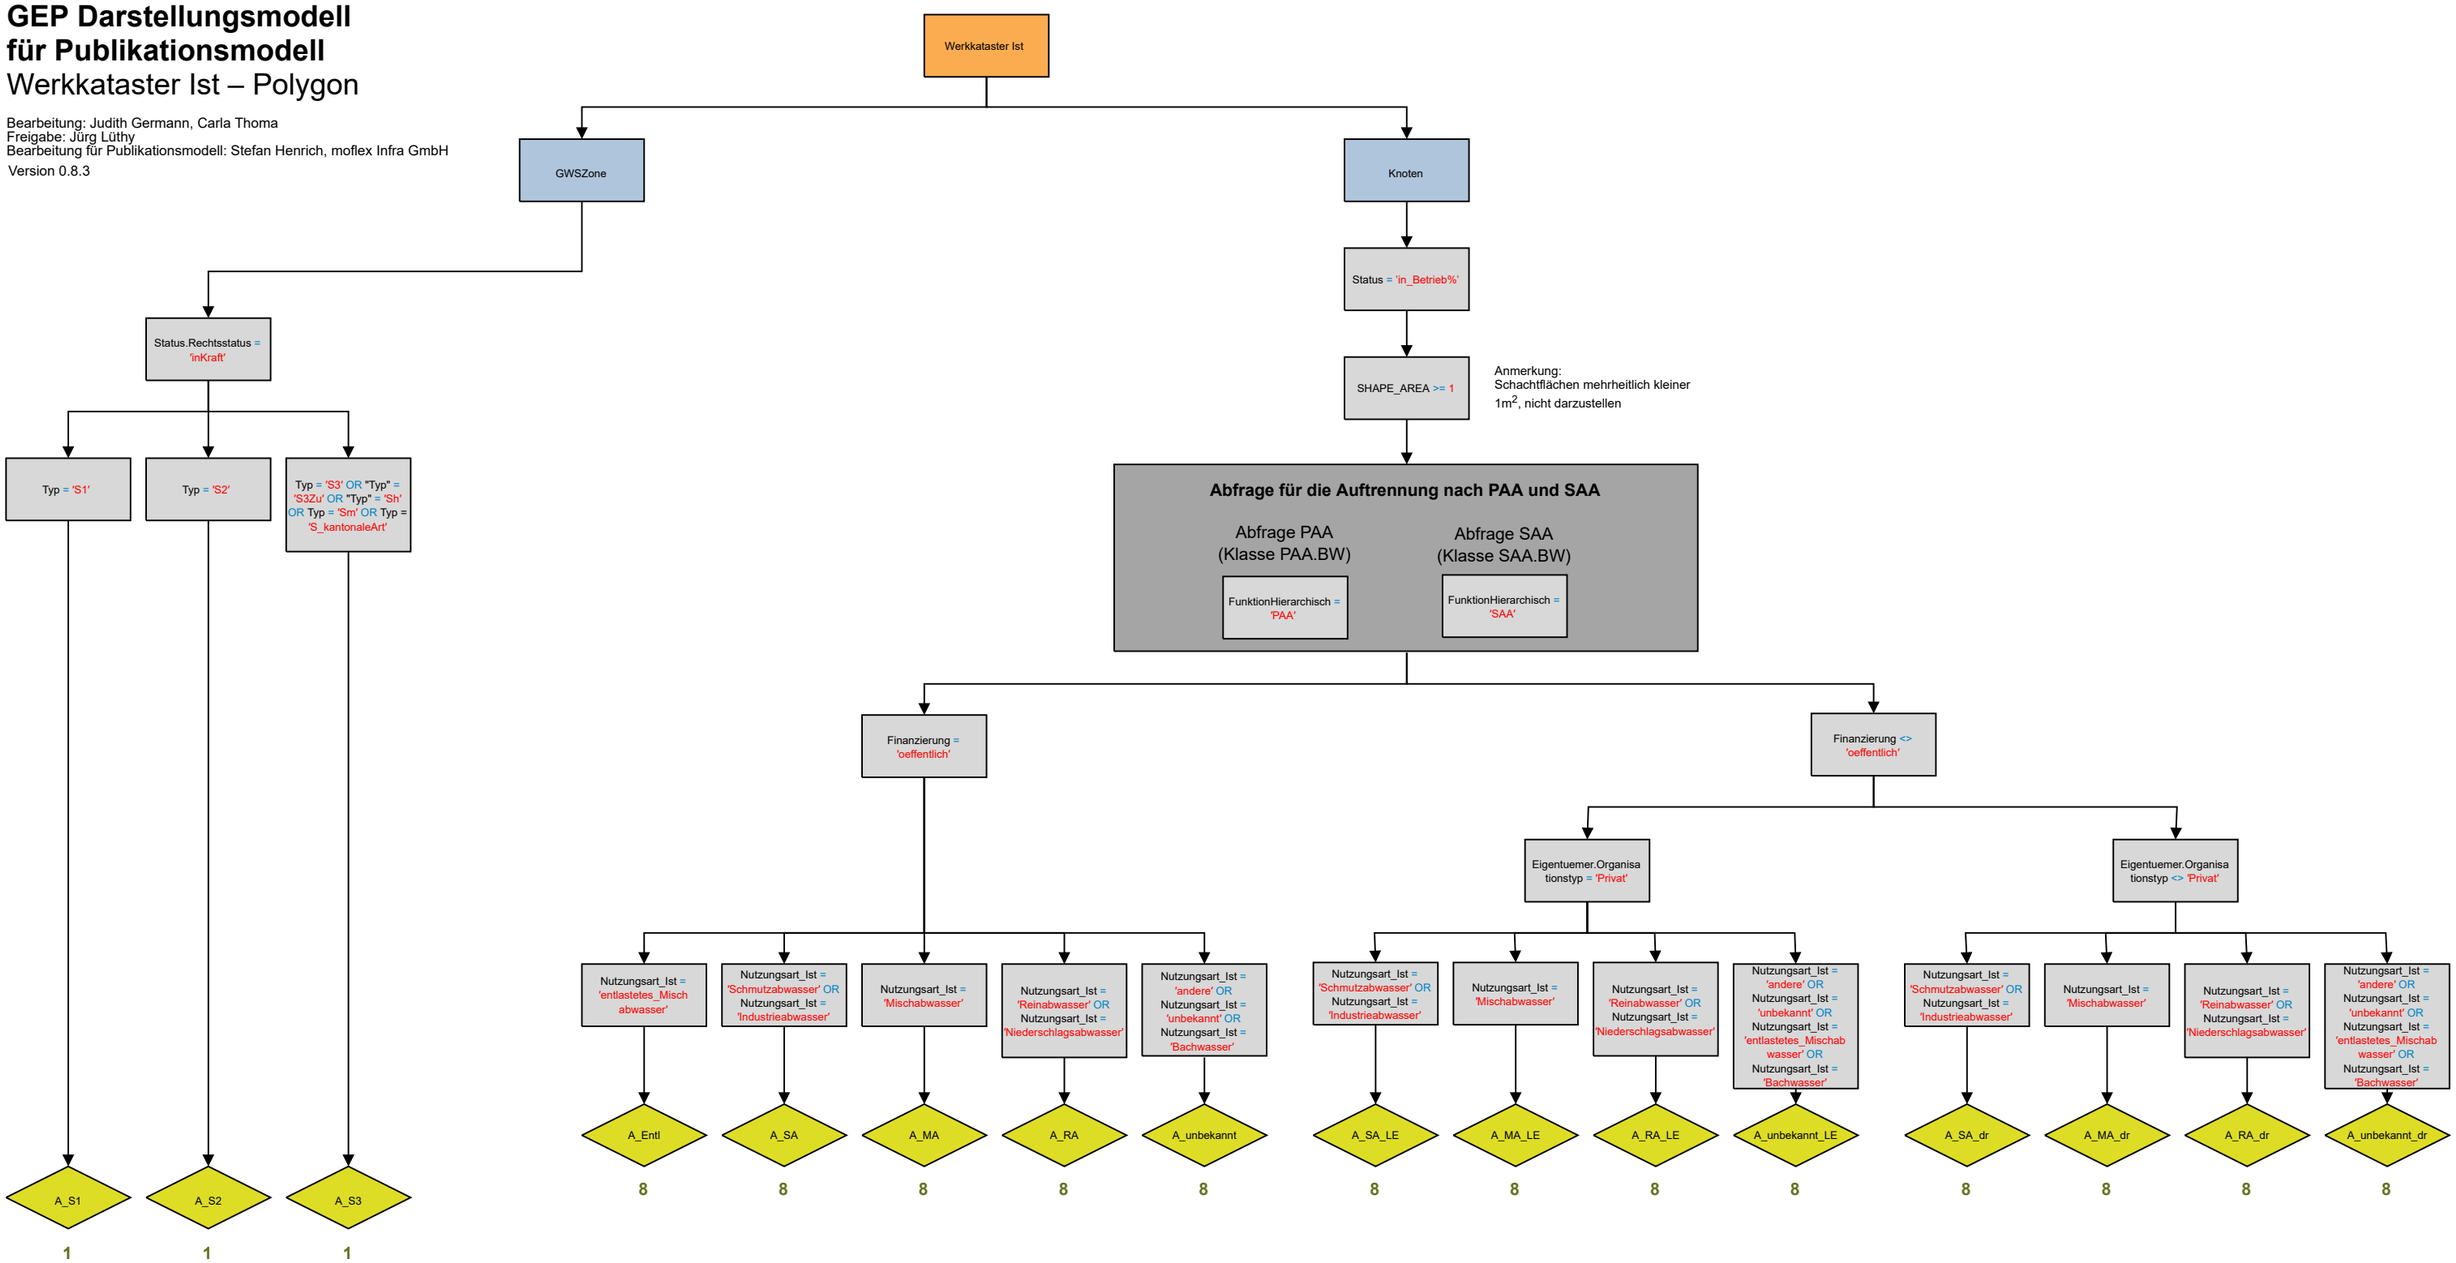


GEP Darstellungsmodell für Publikationsmodell

Werkkataster Ist – Linien

Bearbeitung: Judith Germann, Carla Thoma
Freigabe: Jürg Lüthy
Bearbeitung für Publikationsmodell: Stefan Henrich, moflex Infra GmbH

Version 0.8.3

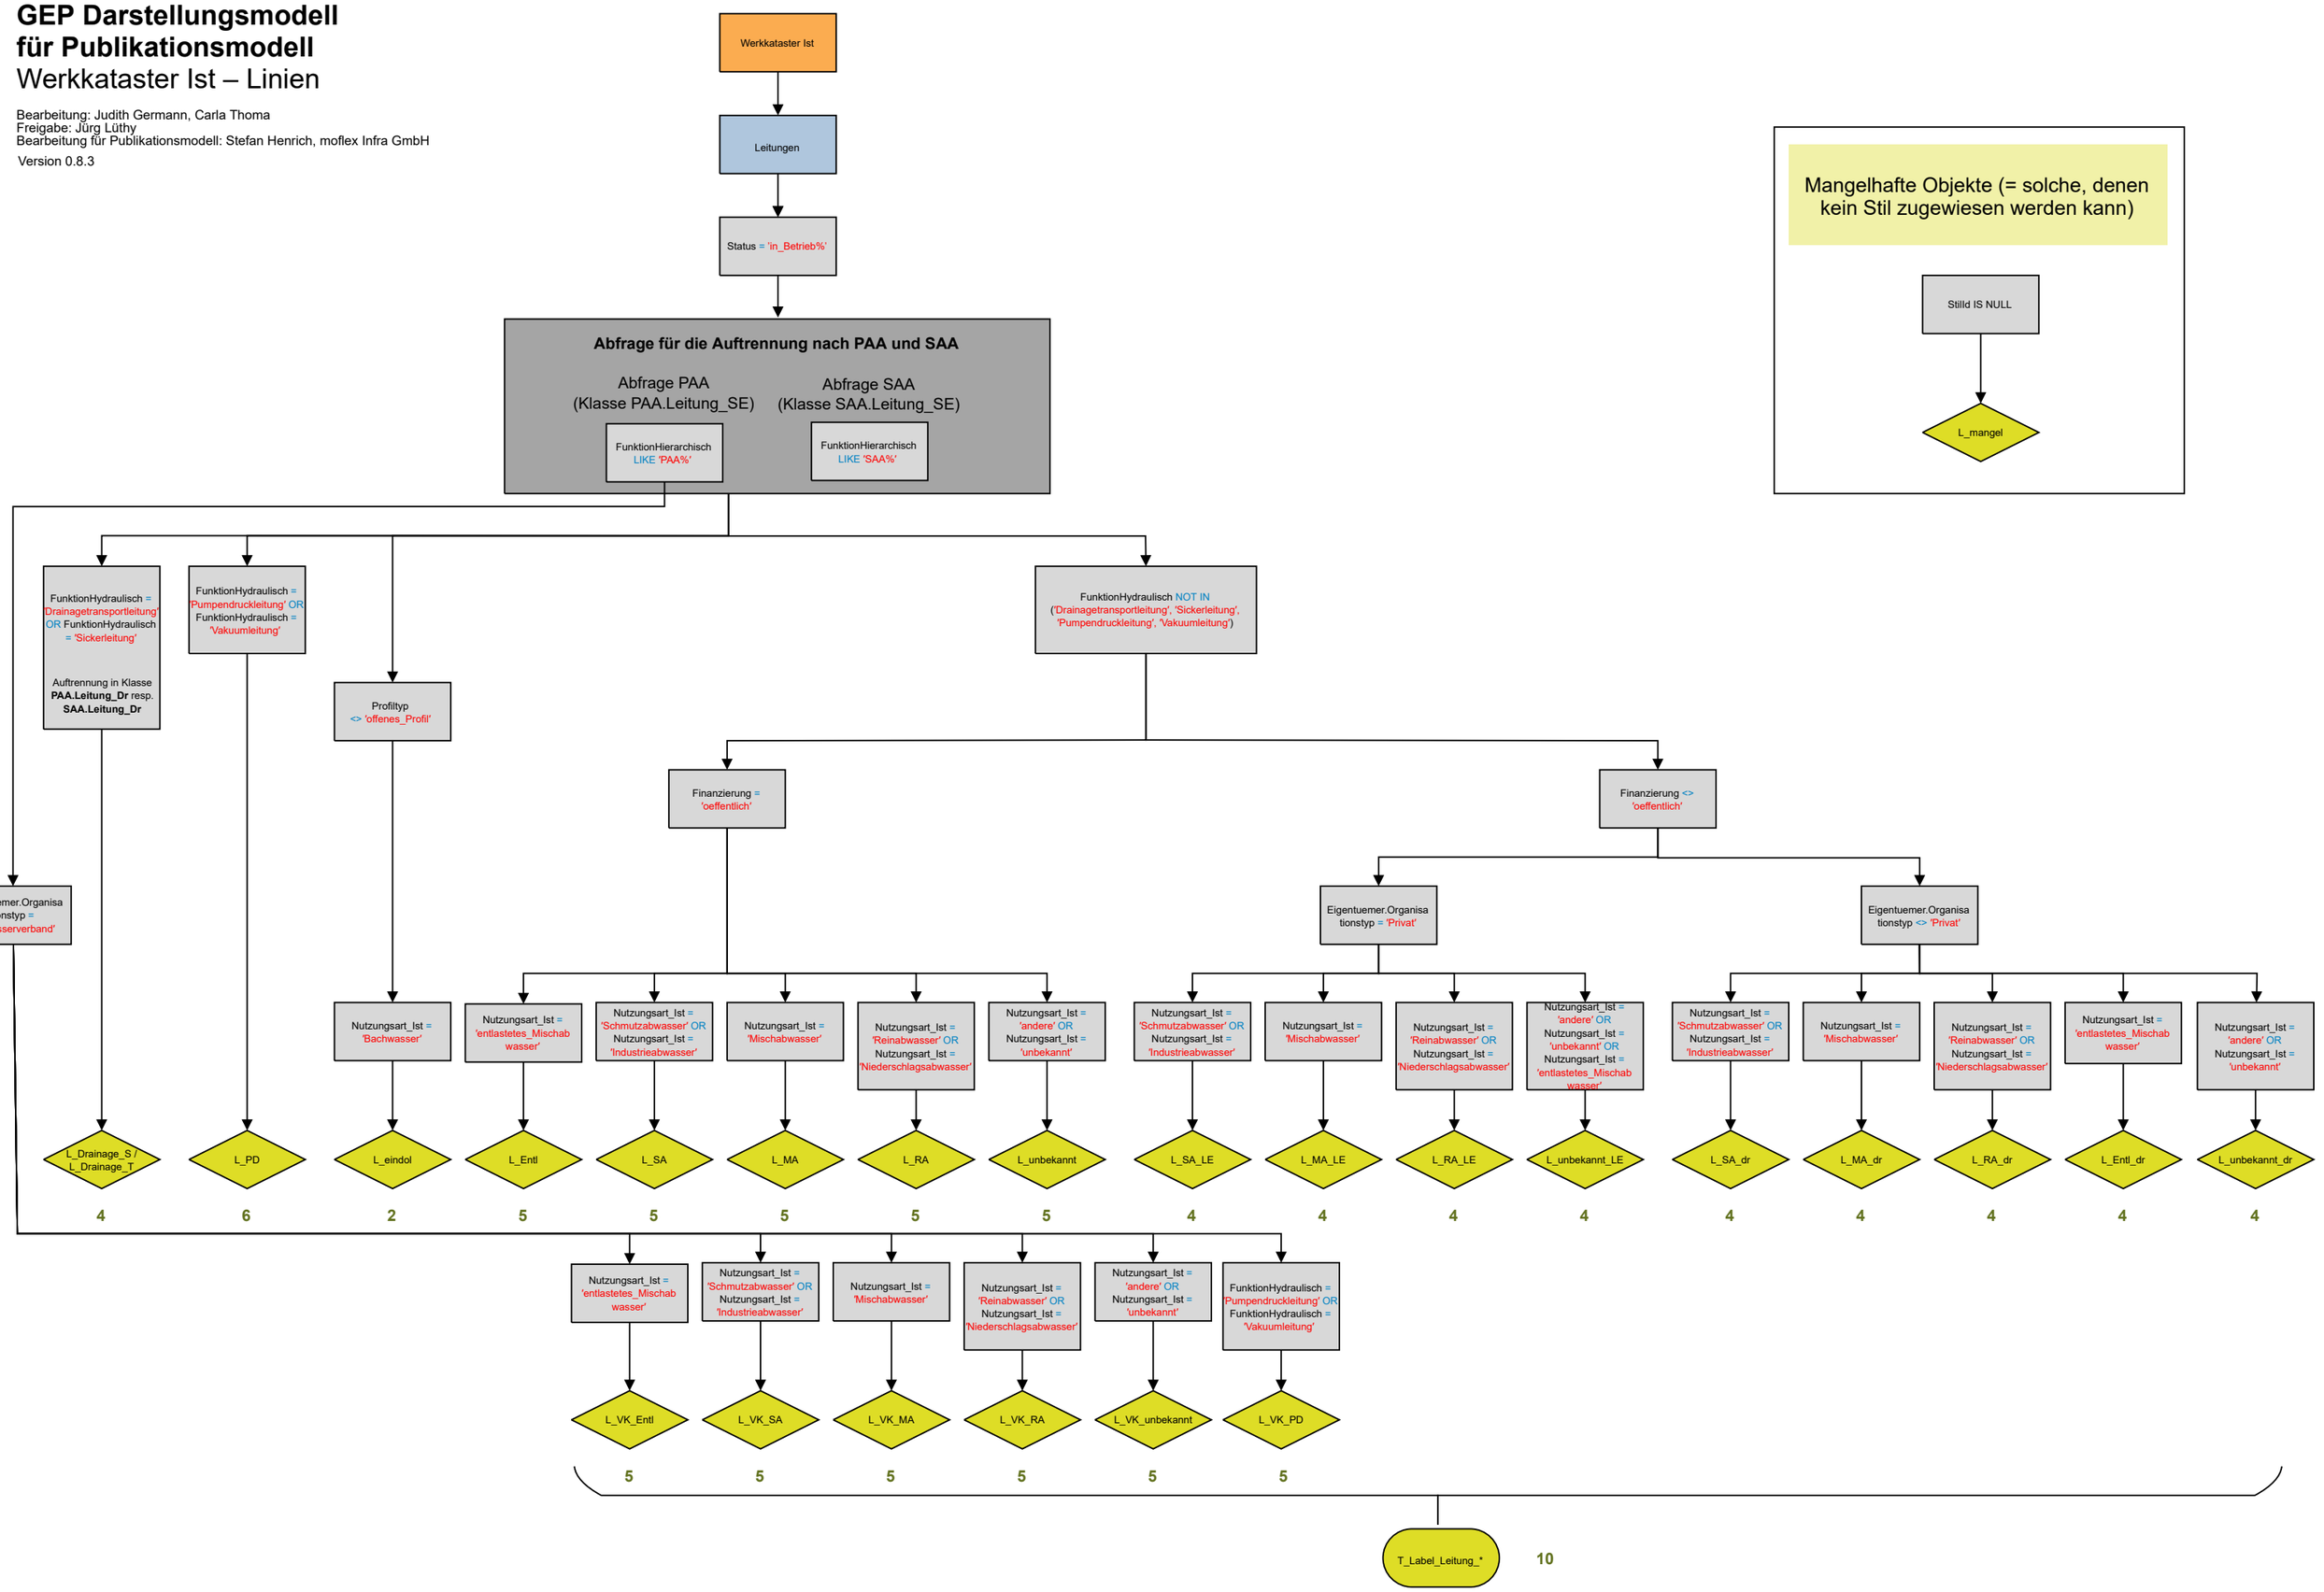


GEP Darstellungsmodell für Publikationsmodell

Werkkataster Ist – Punkt (1/2)

Bearbeitung: Judith Germann, Carla Thoma
Freigabe: Jürg Lüthy
Bearbeitung für Publikationsmodell: Stefan Henrich, moflex Infra GmbH

Version 0.8.3

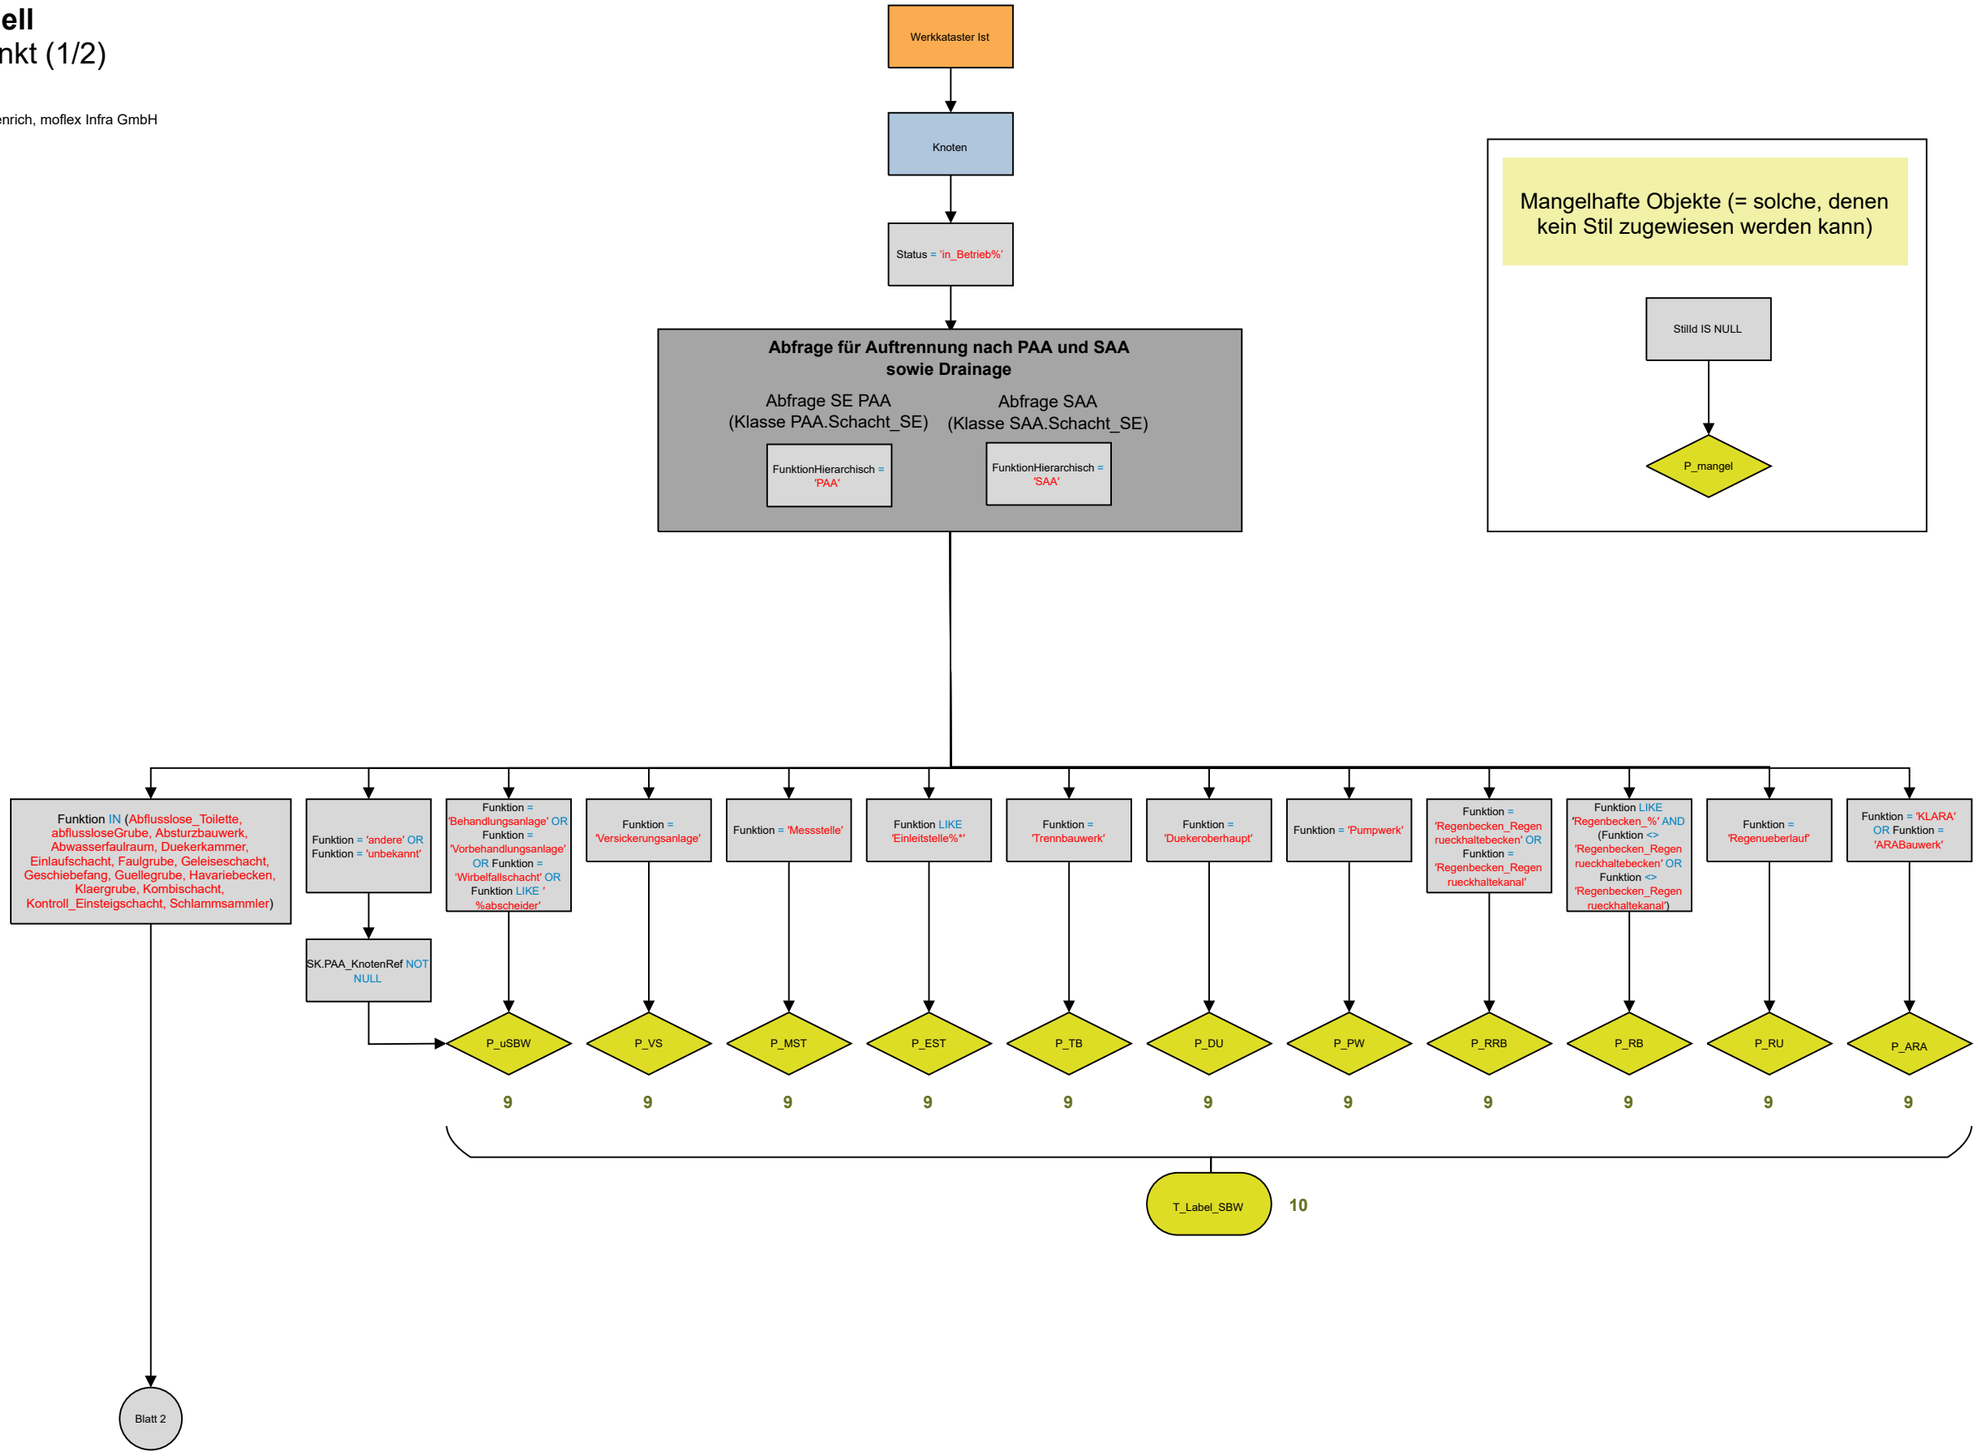


GEP Darstellungsmodell für Publikationsmodell

Werkkataster Ist – Punkt (2/2)

Bearbeitung: Judith Germann, Carla Thoma
Freigabe: Jürg Lüthy
Bearbeitung für Publikationsmodell: Stefan Henrich, moflex Infra GmbH

Version 0.8.3

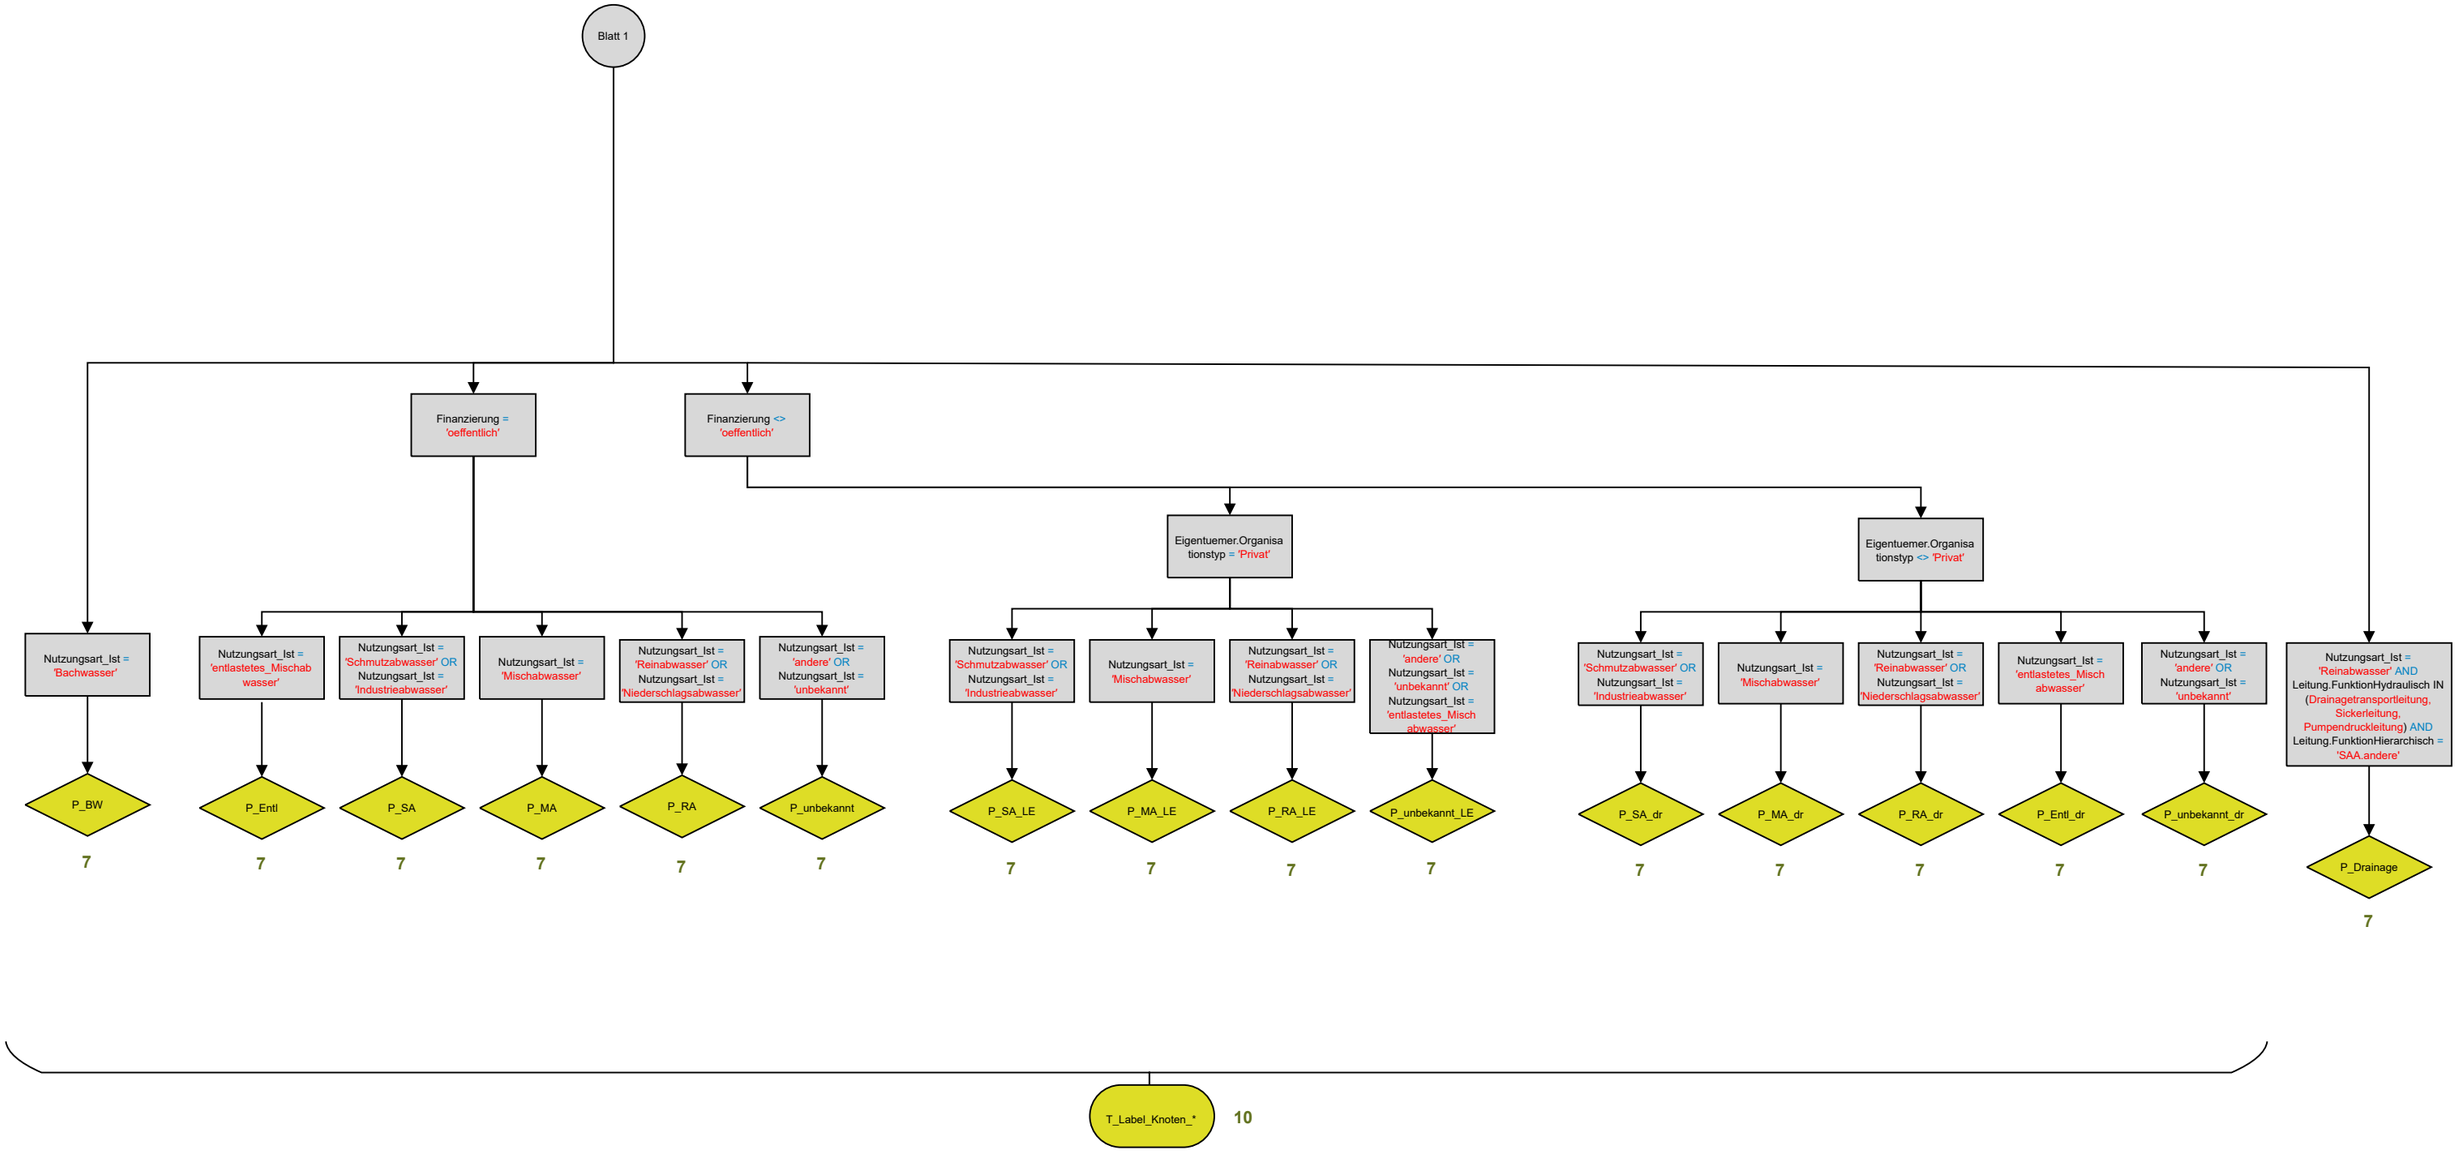


GEP Darstellungsmodell für Publikationsmodell

TEZG Ist – Polygon mit Beschriftung

Bearbeitung: Judith Germann, Carla Thoma
Freigabe: Jürg Lüthy
Bearbeitung für Publikationsmodell: Stefan Henrich, moflex Infra GmbH

Version 0.8.3

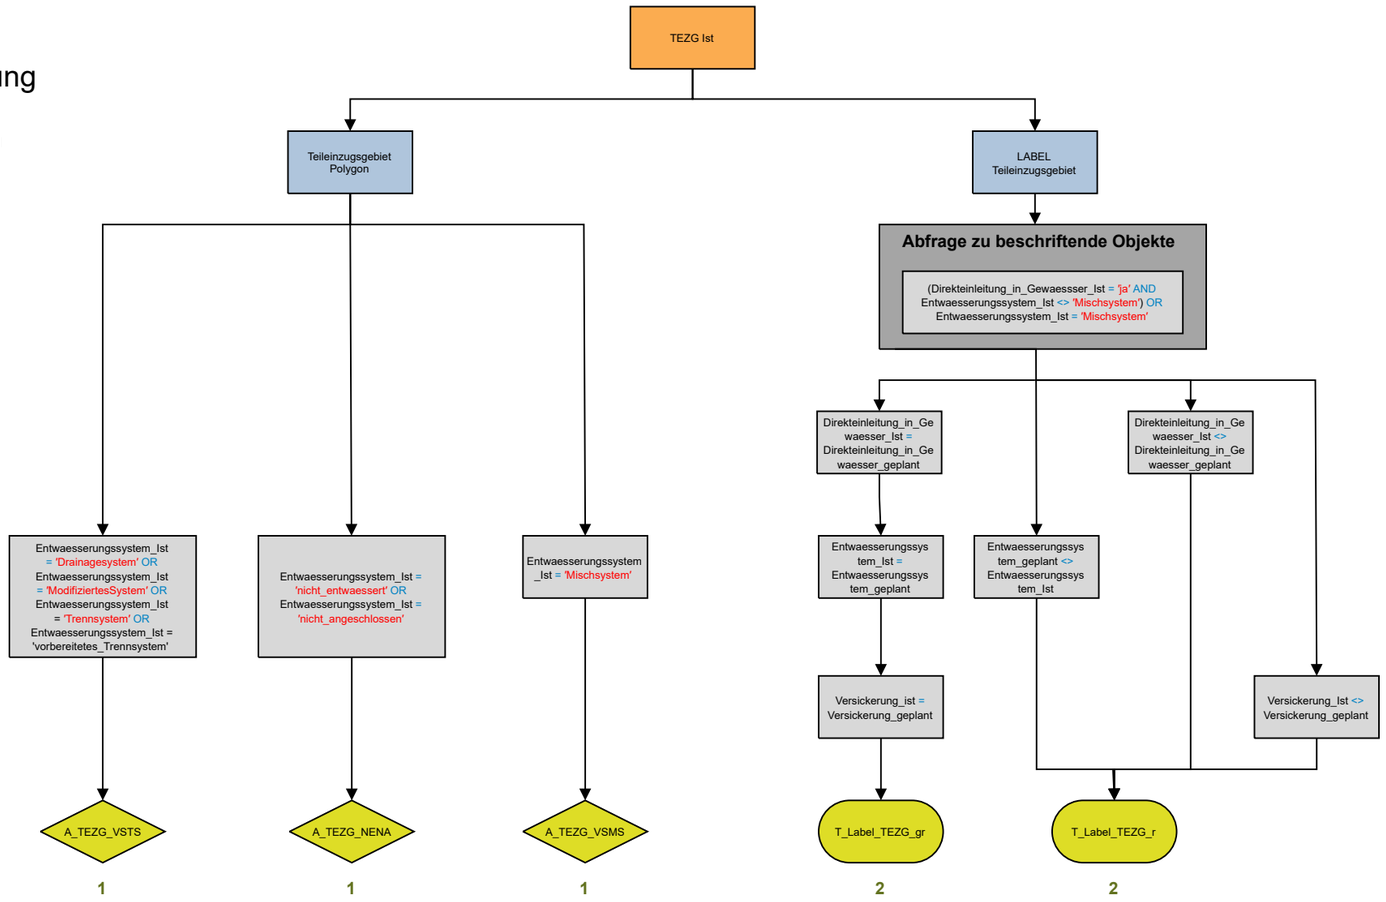


GEP Darstellungsmodell für Publikationsmodell

TEZG Soll – Polygon mit Beschriftung

Bearbeitung: Judith Germann, Carla Thoma
Freigabe: Jürg Lüthy
Bearbeitung für Publikationsmodell: Stefan Henrich, moflex Infra GmbH

Version 0.8.3

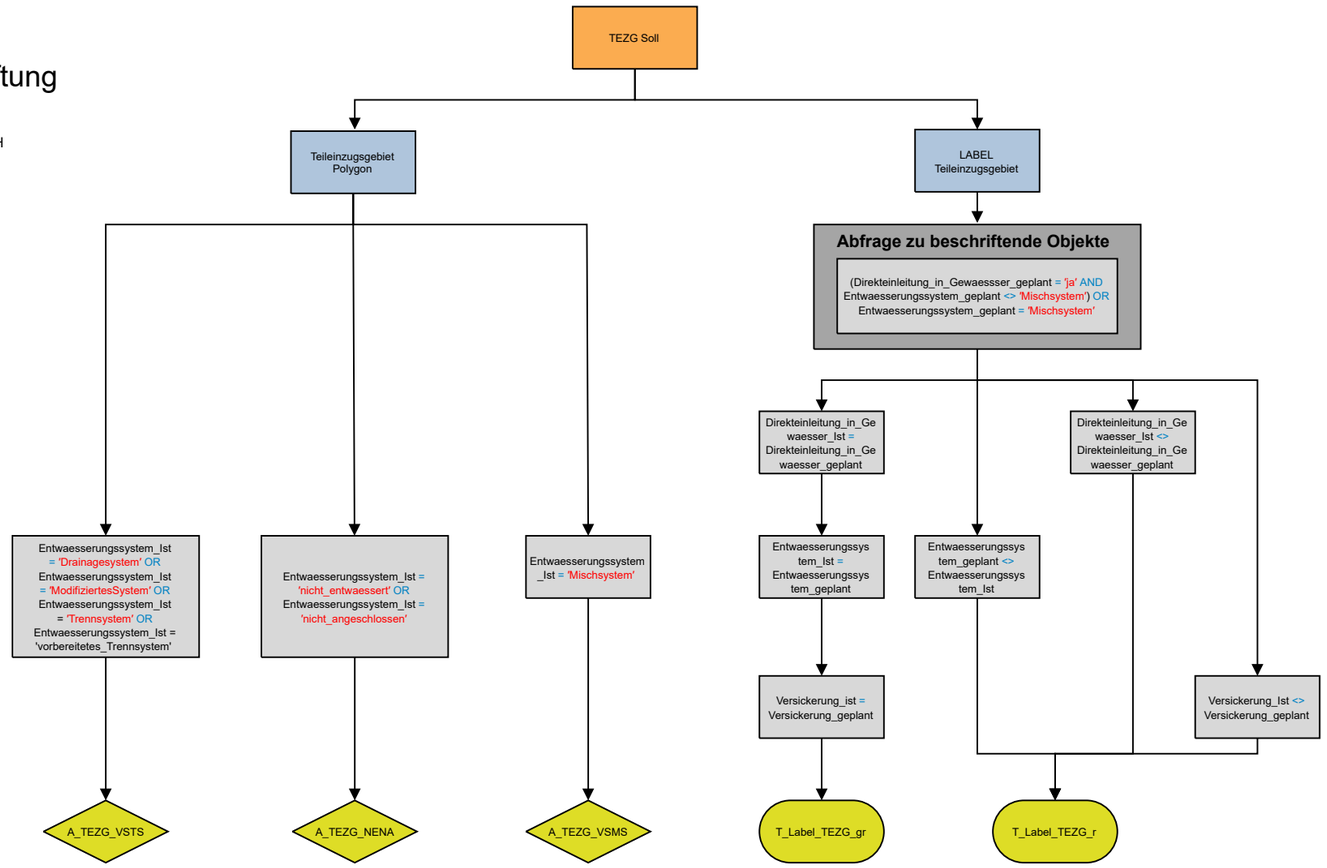


GEP Darstellungsmodell für Publikationsmodell

Massnahmenplan


Bearbeitung: Judith Germann, Carla Thoma
Freigabe: Jürg Lüthy
Bearbeitung für Publikationsmodell: Stefan Henrich, moflex Infra GmbH

Version 0.8.3

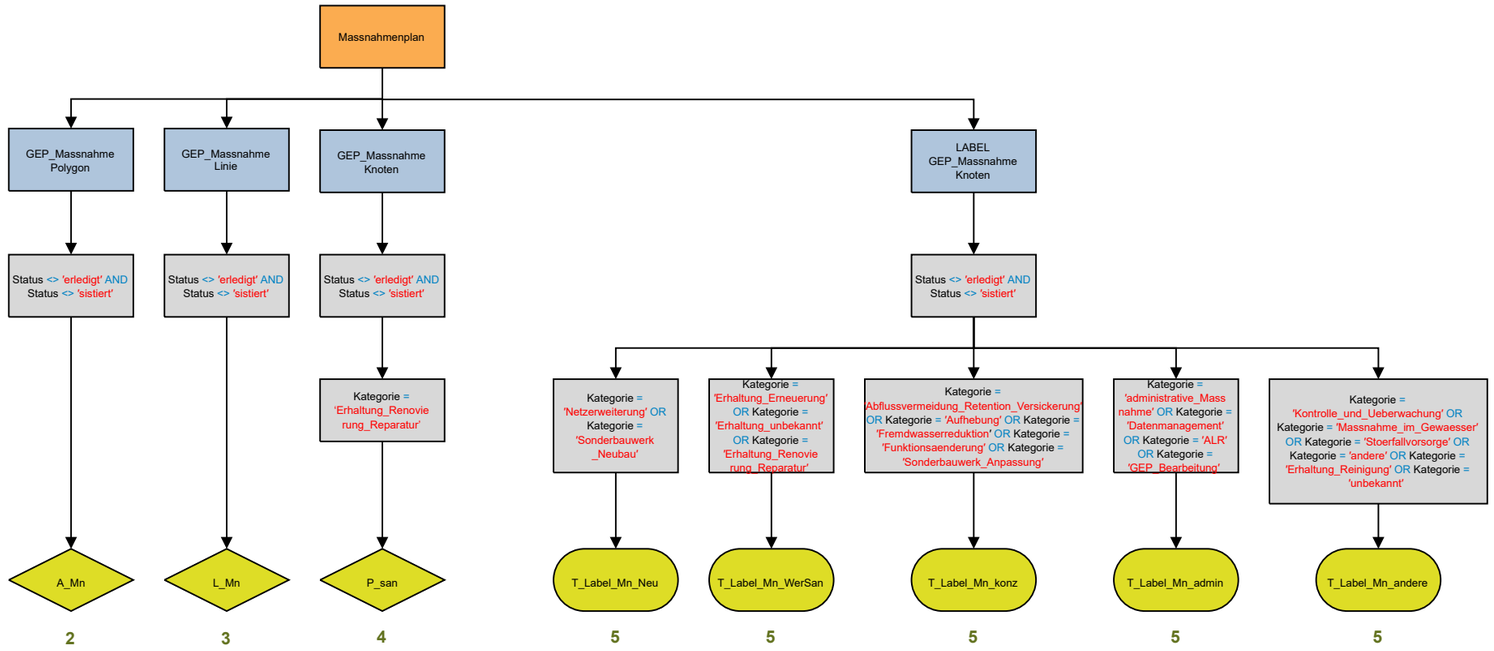

GEP Darstellungsmodell
für Publikationsmodell
Abwasserbehandlung ländlicher Raum (ALR)

Bearbeitung: Judith Germann, Carla Thoma
Freigabe: Jürg Lüthy
Bearbeitung für Publikationsmodell: Stefan Henrich, moflex Infra GmbH
Version 0.8.3

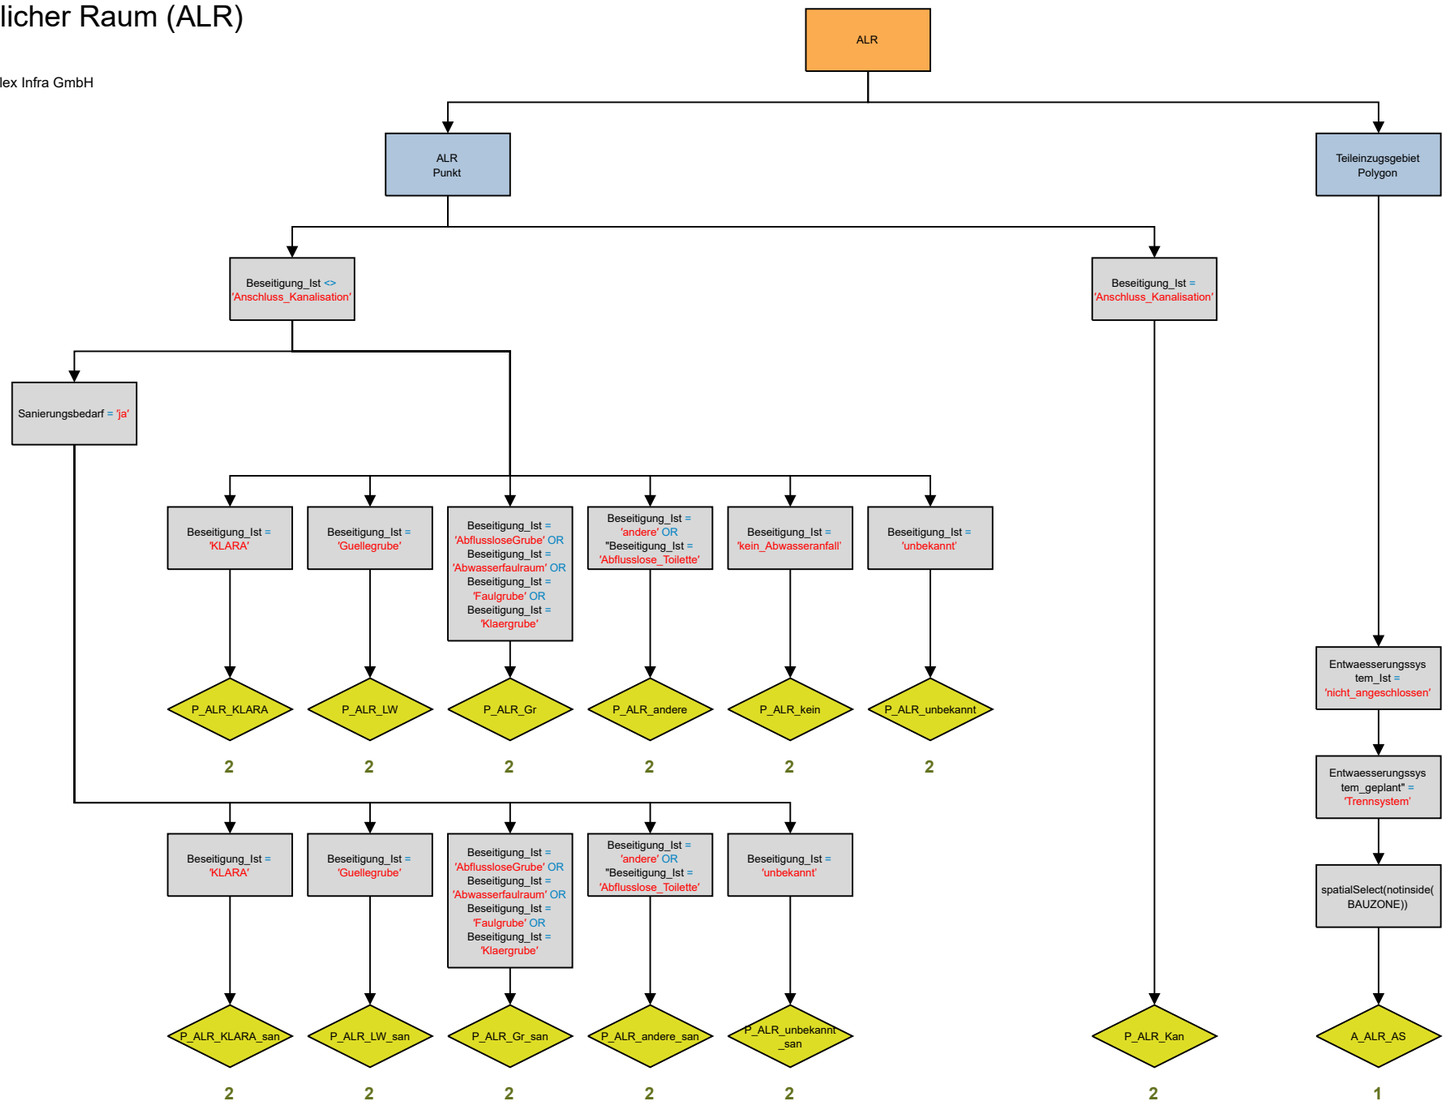


GEP Darstellungsmodell für Publikationsmodell

Zustandsplan Kanalisation - Polygon

Bearbeitung: Judith Germann, Carla Thoma
Freigabe: Jürg Lüthy
Bearbeitung für Publikationsmodell: Stefan Henrich, moflex Infra GmbH

Version 0.8.3

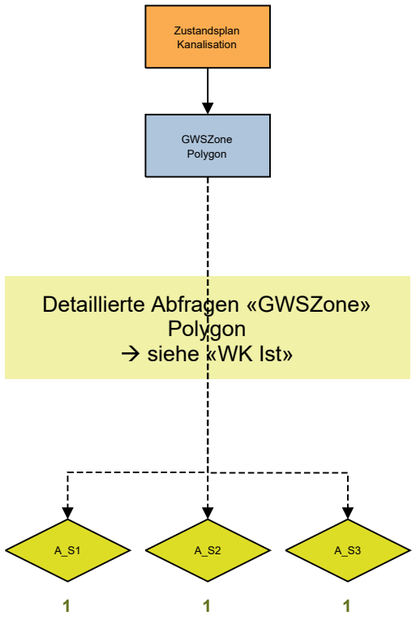


GEP Darstellungsmodell für Publikationsmodell

Zustandsplan Kanalisation - Linien

Bearbeitung: Judith Germann, Carla Thoma
Freigabe: Jürg Lüthy
Bearbeitung für Publikationsmodell: Stefan Henrich, moflex Infra GmbH

Version 0.8.3

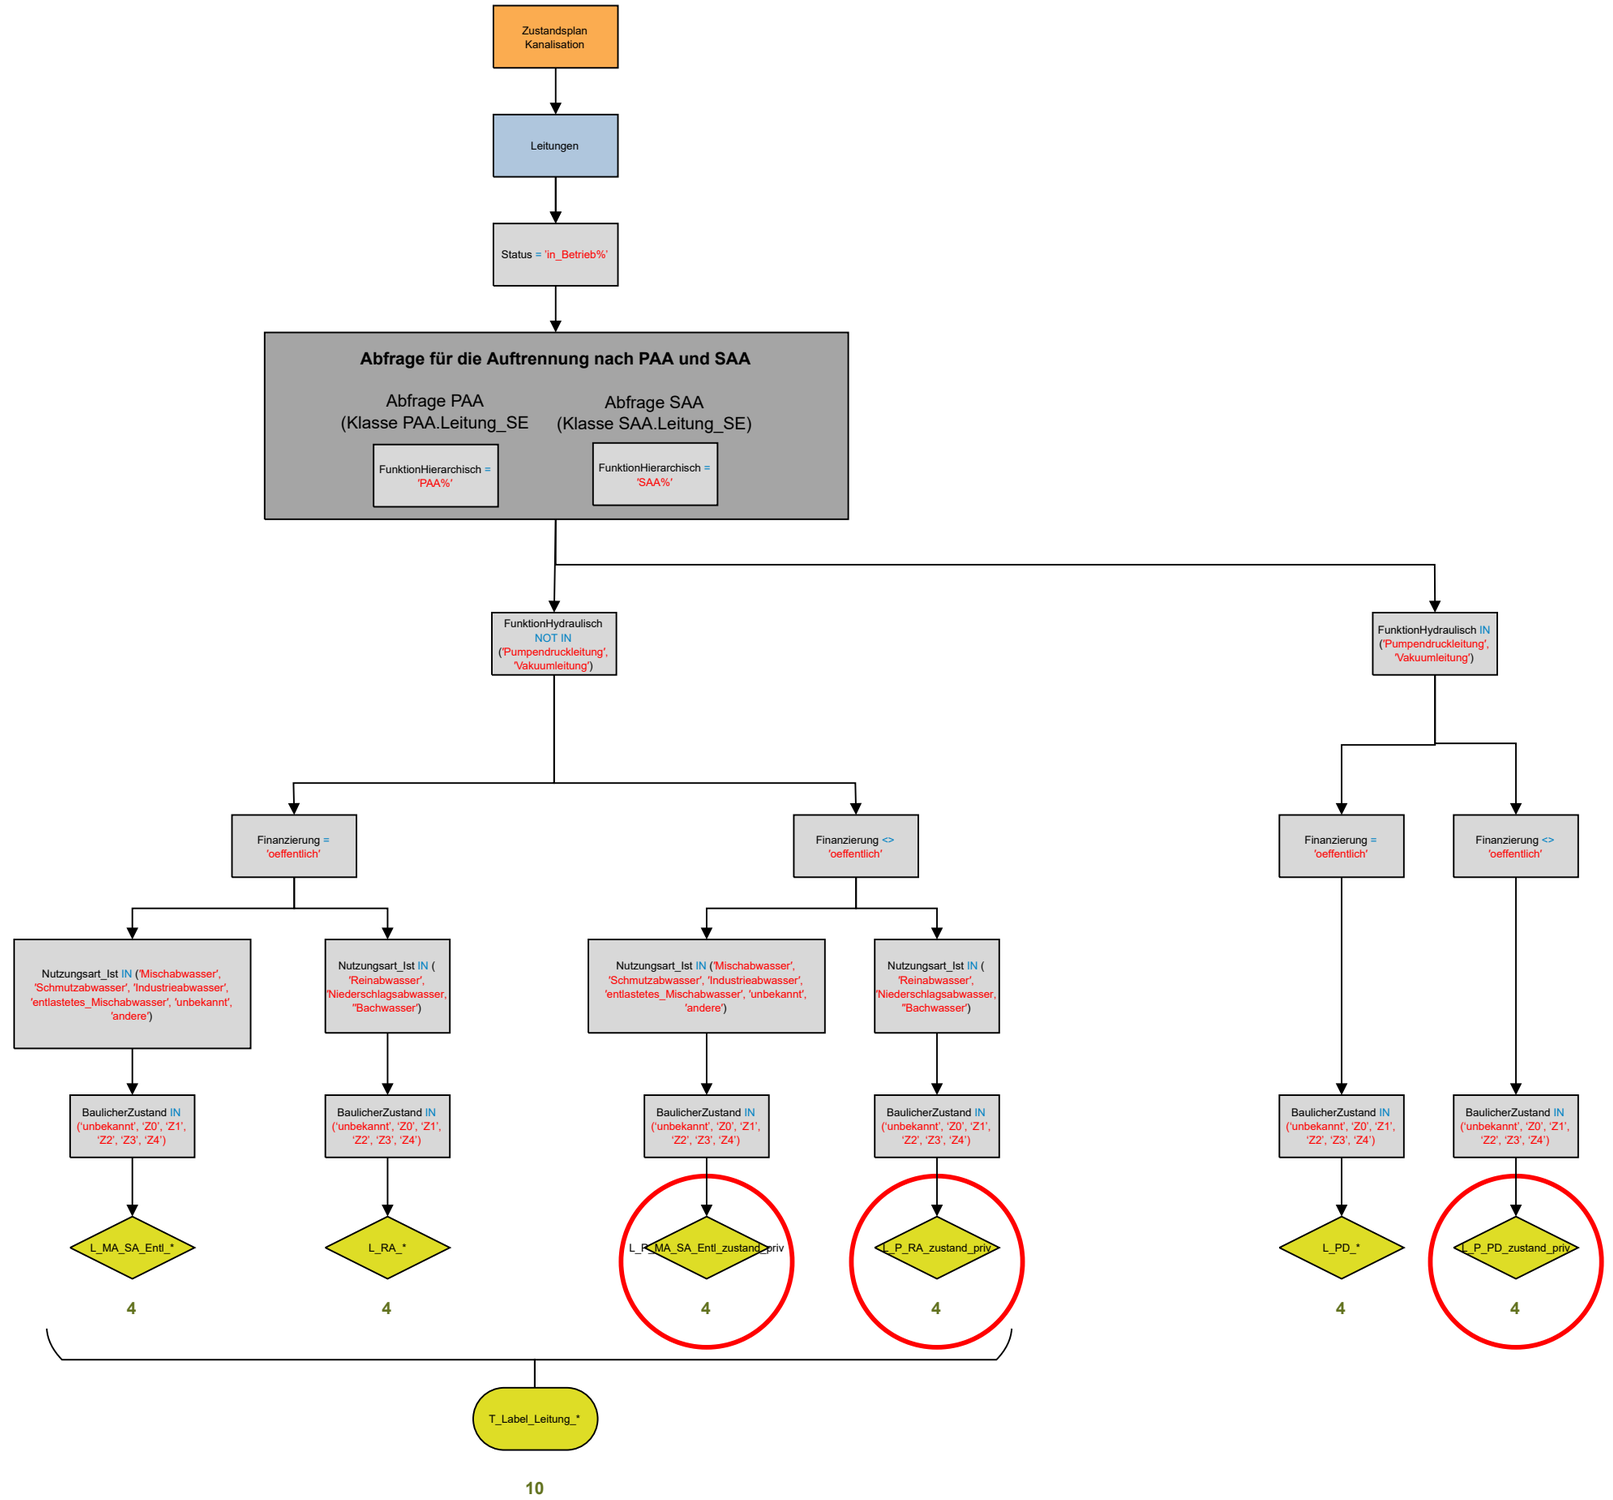


GEP Darstellungsmodell für Publikationsmodell

Zustandsplan Kanalisation - Punkt

Bearbeitung: Judith Germann, Carla Thoma
Freigabe: Jürg Lüthy
Bearbeitung für Publikationsmodell: Stefan Henrich, moflex Infra GmbH

Version 0.8.3

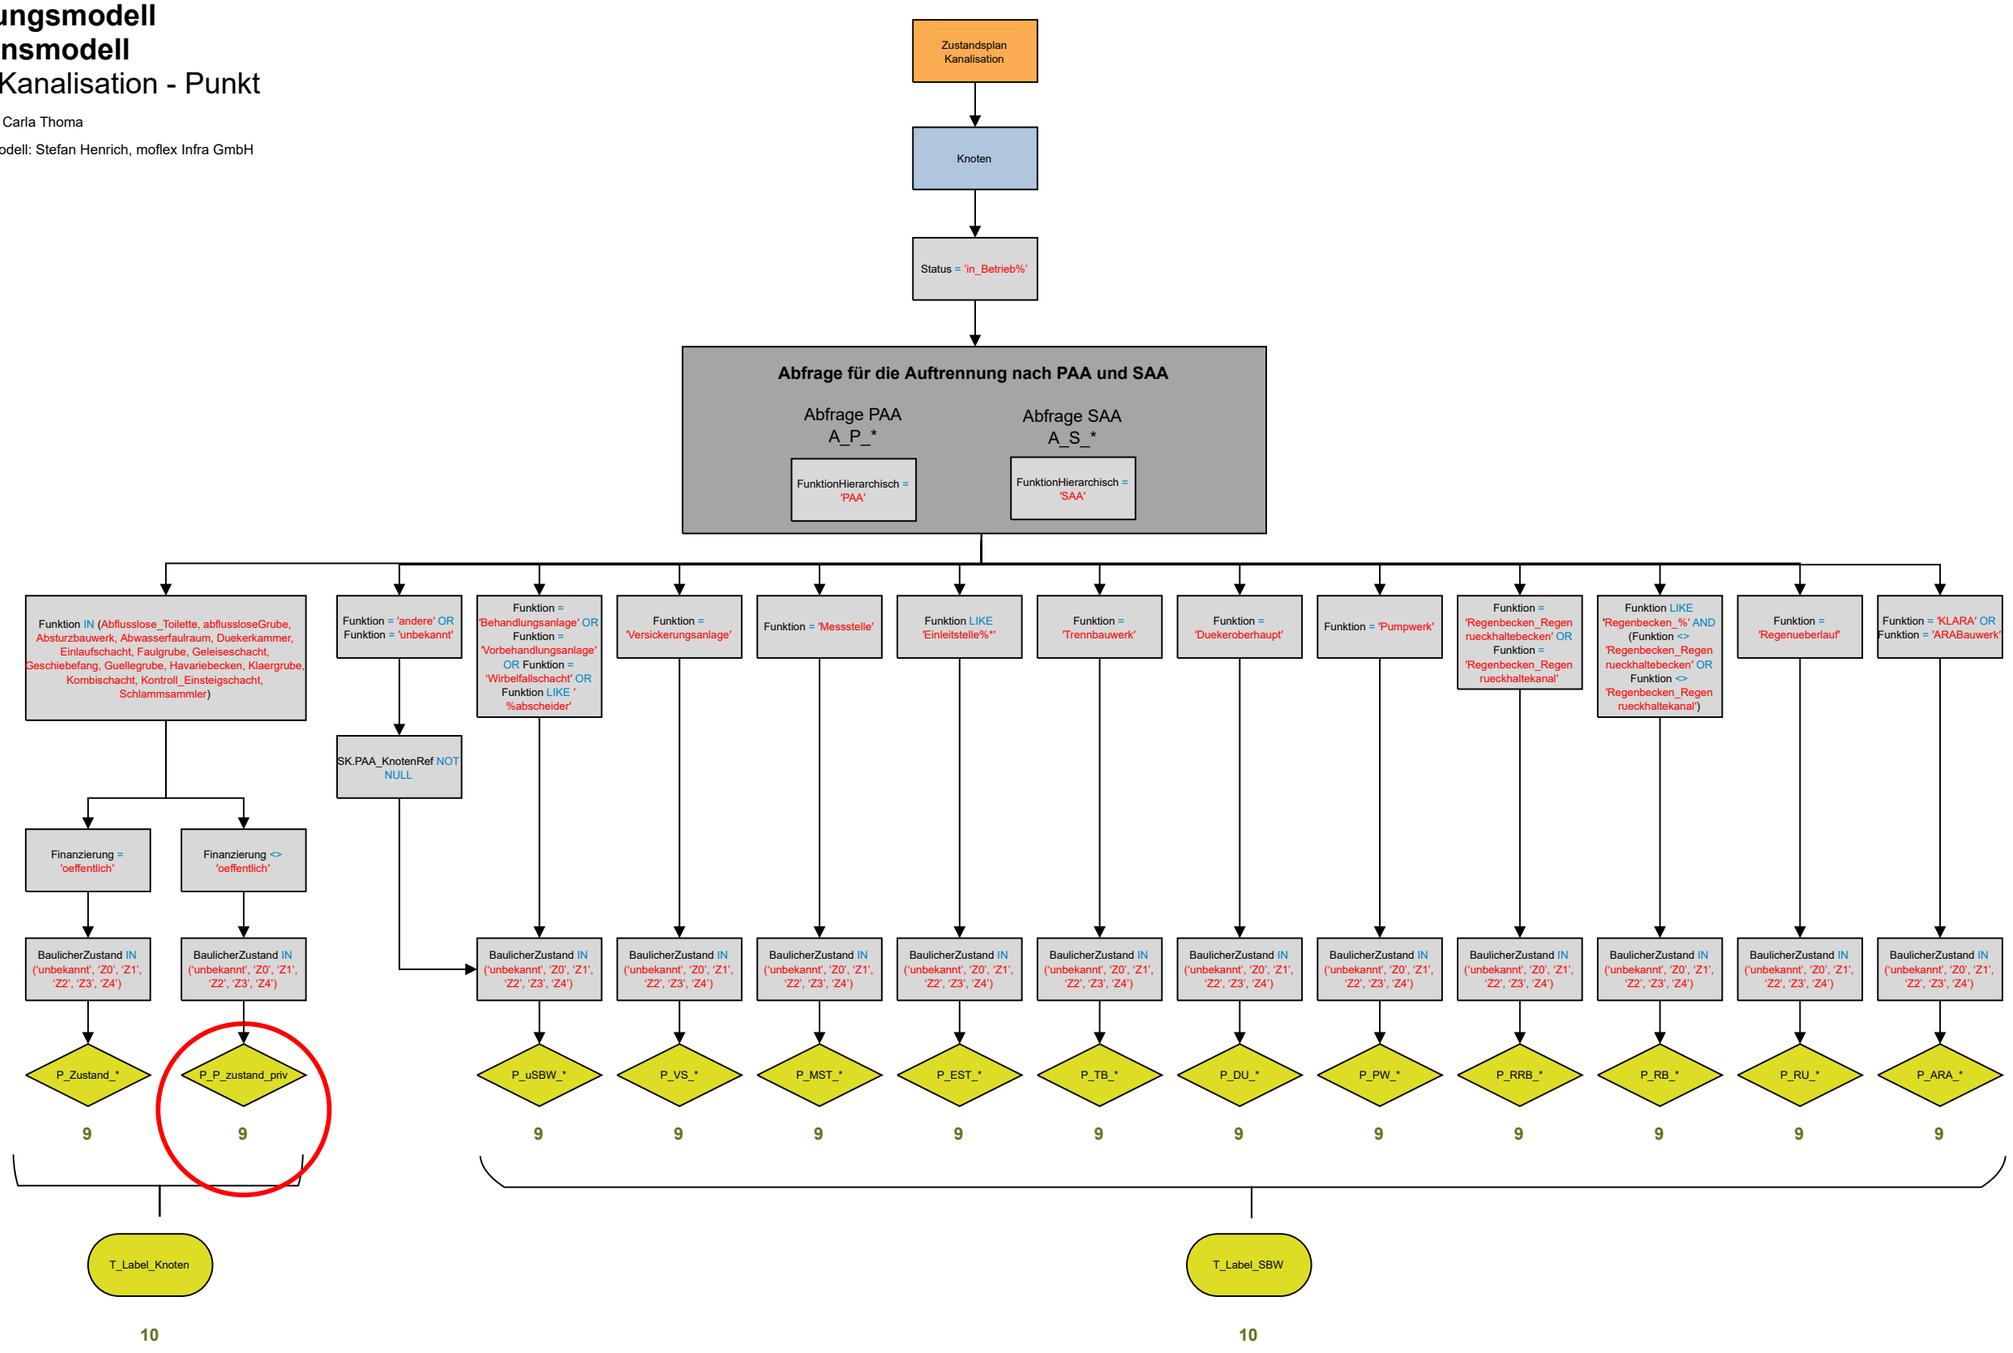


GEP Darstellungsmodell für Publikationsmodell

Erschliessungsplan - Polygon


Bearbeitung: Judith Germann, Carla Thoma
Freigabe: Jürg Lüthy
Bearbeitung für Publikationsmodell: Stefan Henrich, moflex Infra GmbH

Version 0.8.3

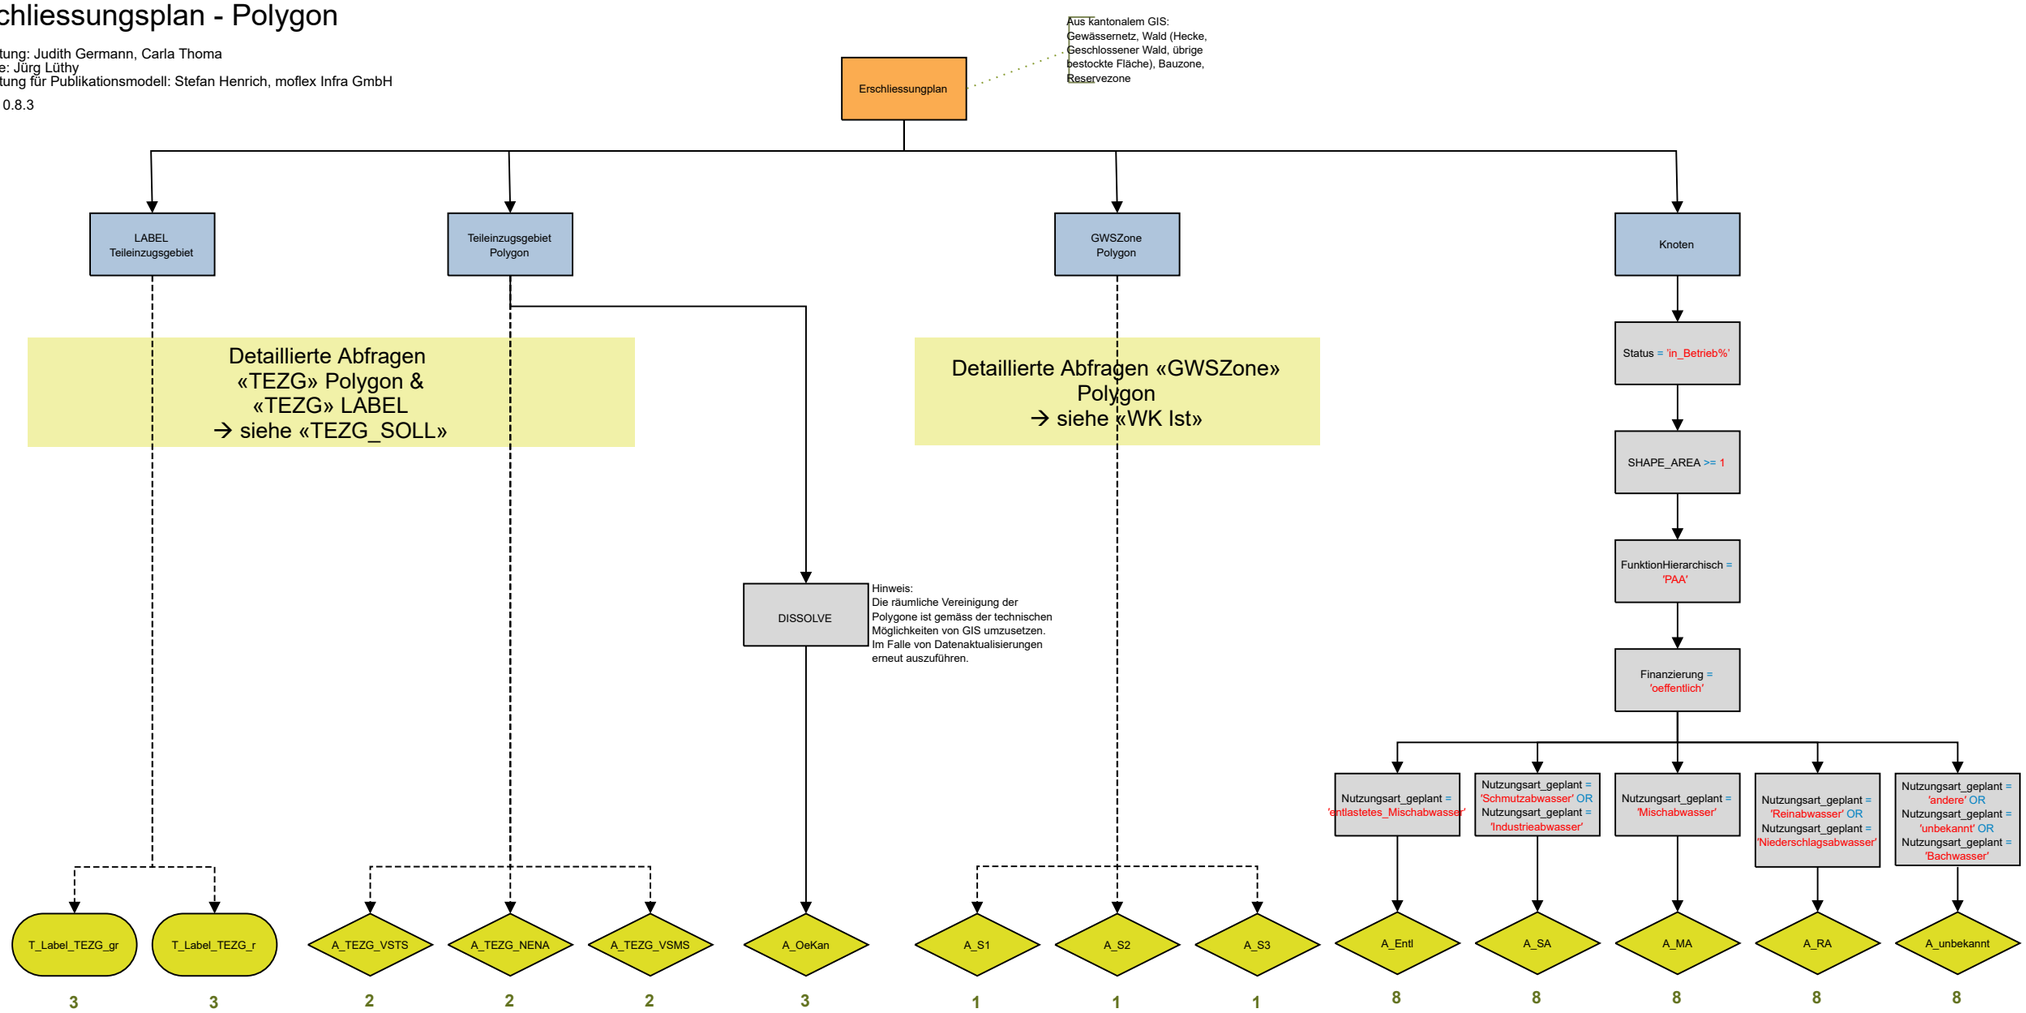


GEP Darstellungsmodell
für Publikationsmodell
Erschliessungsplan - Linie (1/2)

Bearbeitung: Judith Germann, Carla Thoma
Freigabe: Jürg Lüthy
Bearbeitung für Publikationsmodell: Stefan Henrich, moflex Infra GmbH
Version 0.8.3

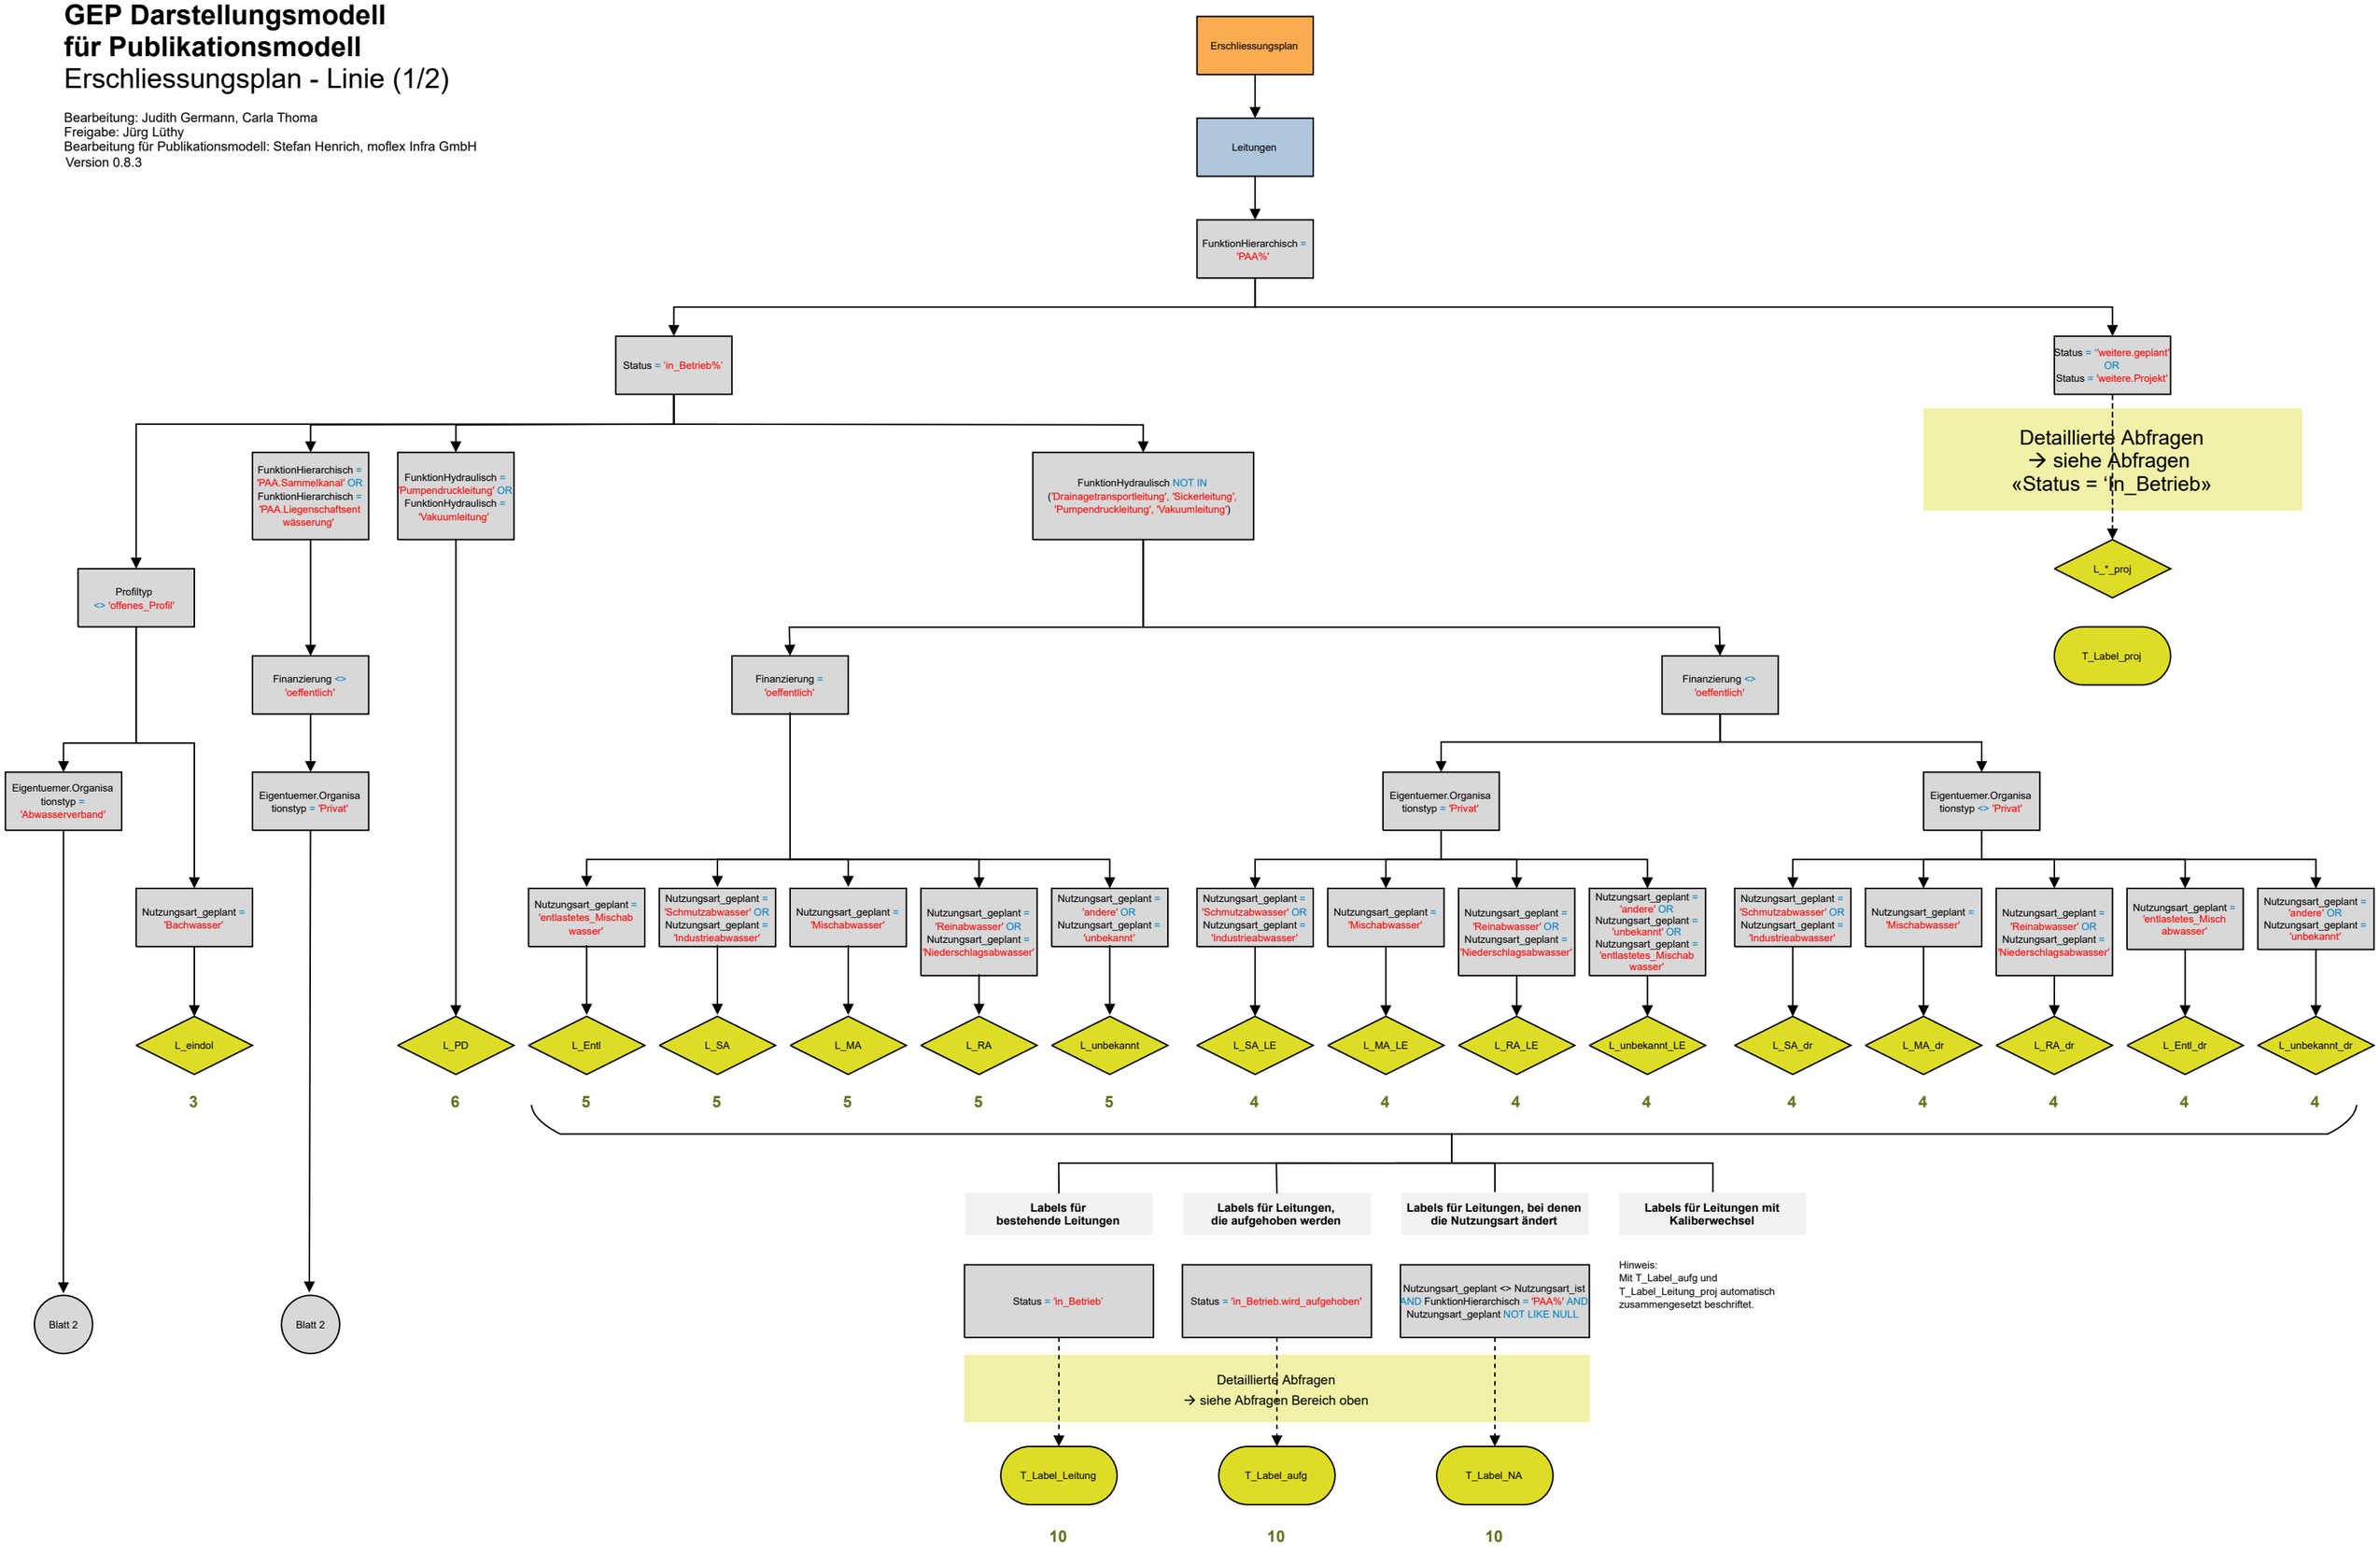

GEP Darstellungsmodell
für Publikationsmodell
Erschliessungsplan - Linie (2/2)


Bearbeitung: Judith Germann, Carla Thoma
Freigabe: Jürg Lüthy
Bearbeitung für Publikationsmodell: Stefan Henrich, moflex Infra GmbH
Version 0.8.3

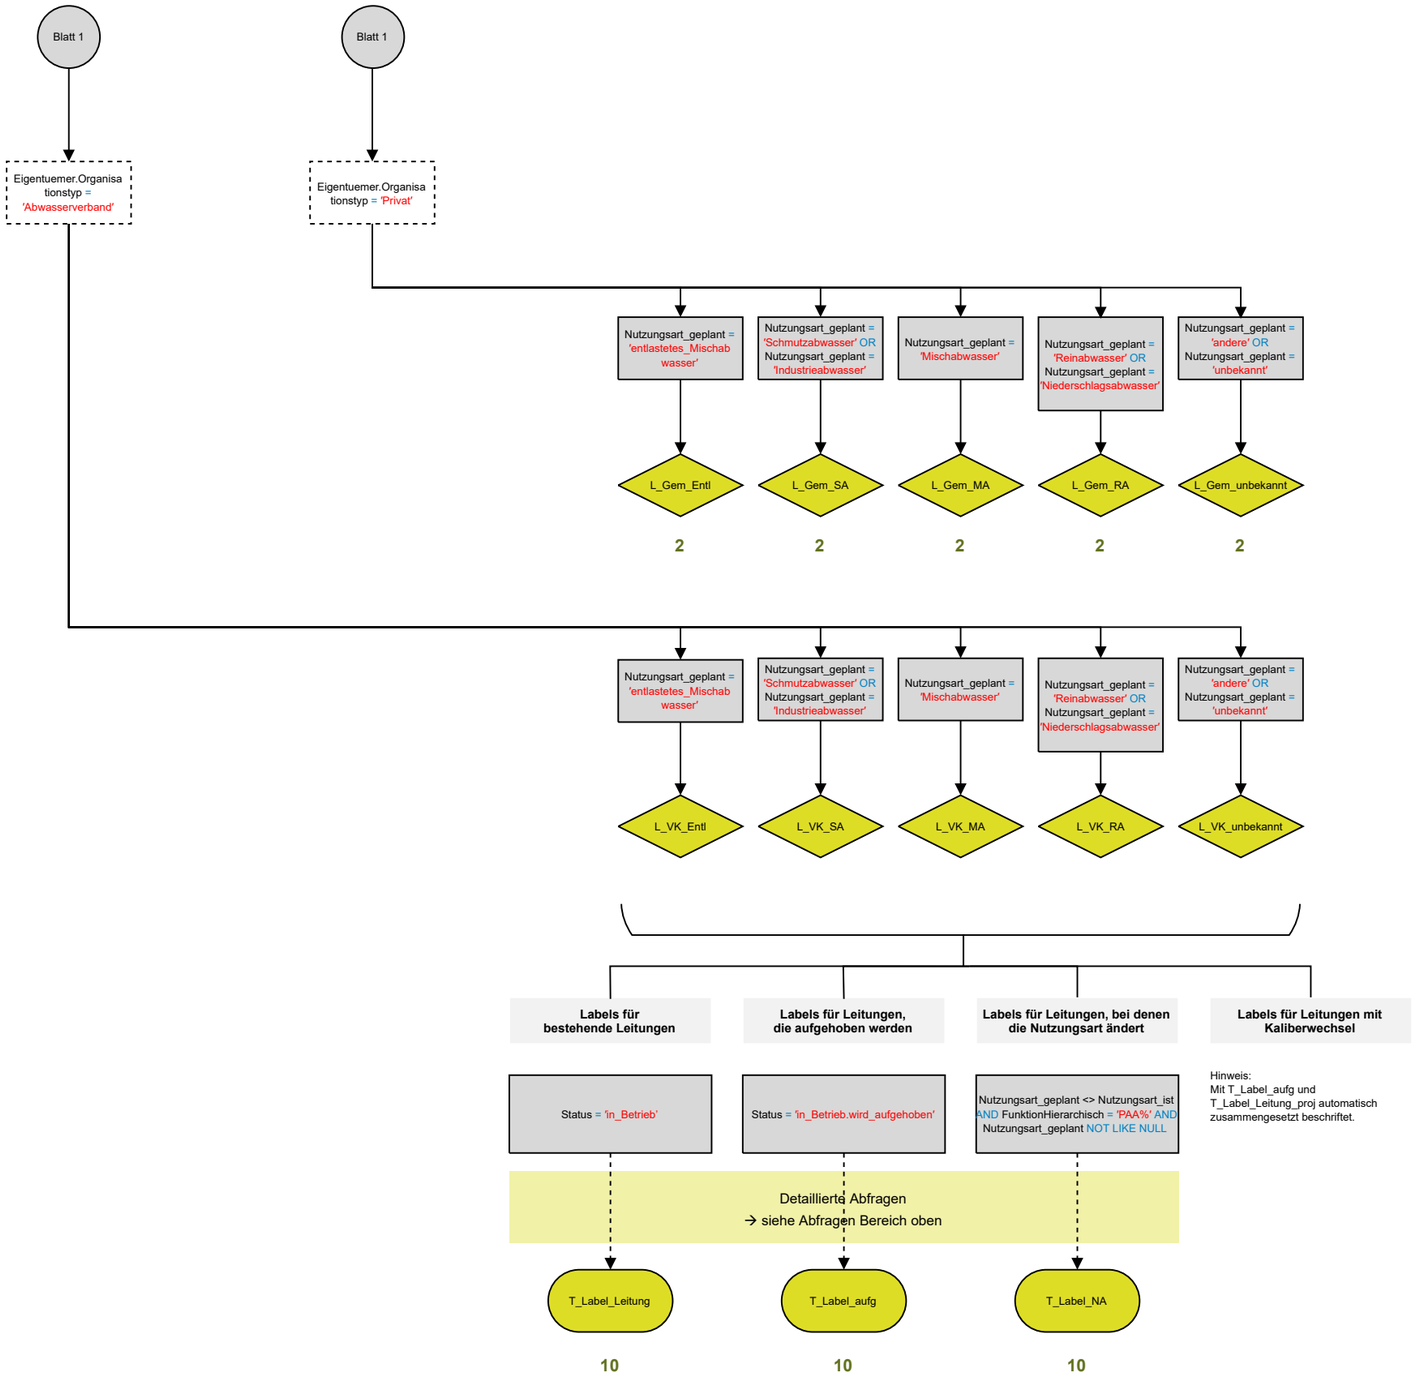

GEP Darstellungsmodell für Publikationsmodell

Erschliessungsplan – Punkt (1/2)

Bearbeitung: Judith Germann, Carla Thoma
Freigabe: Jürg Lüthy
Bearbeitung für Publikationsmodell: Stefan Henrich, moflex Infra GmbH
Version 0.8.3

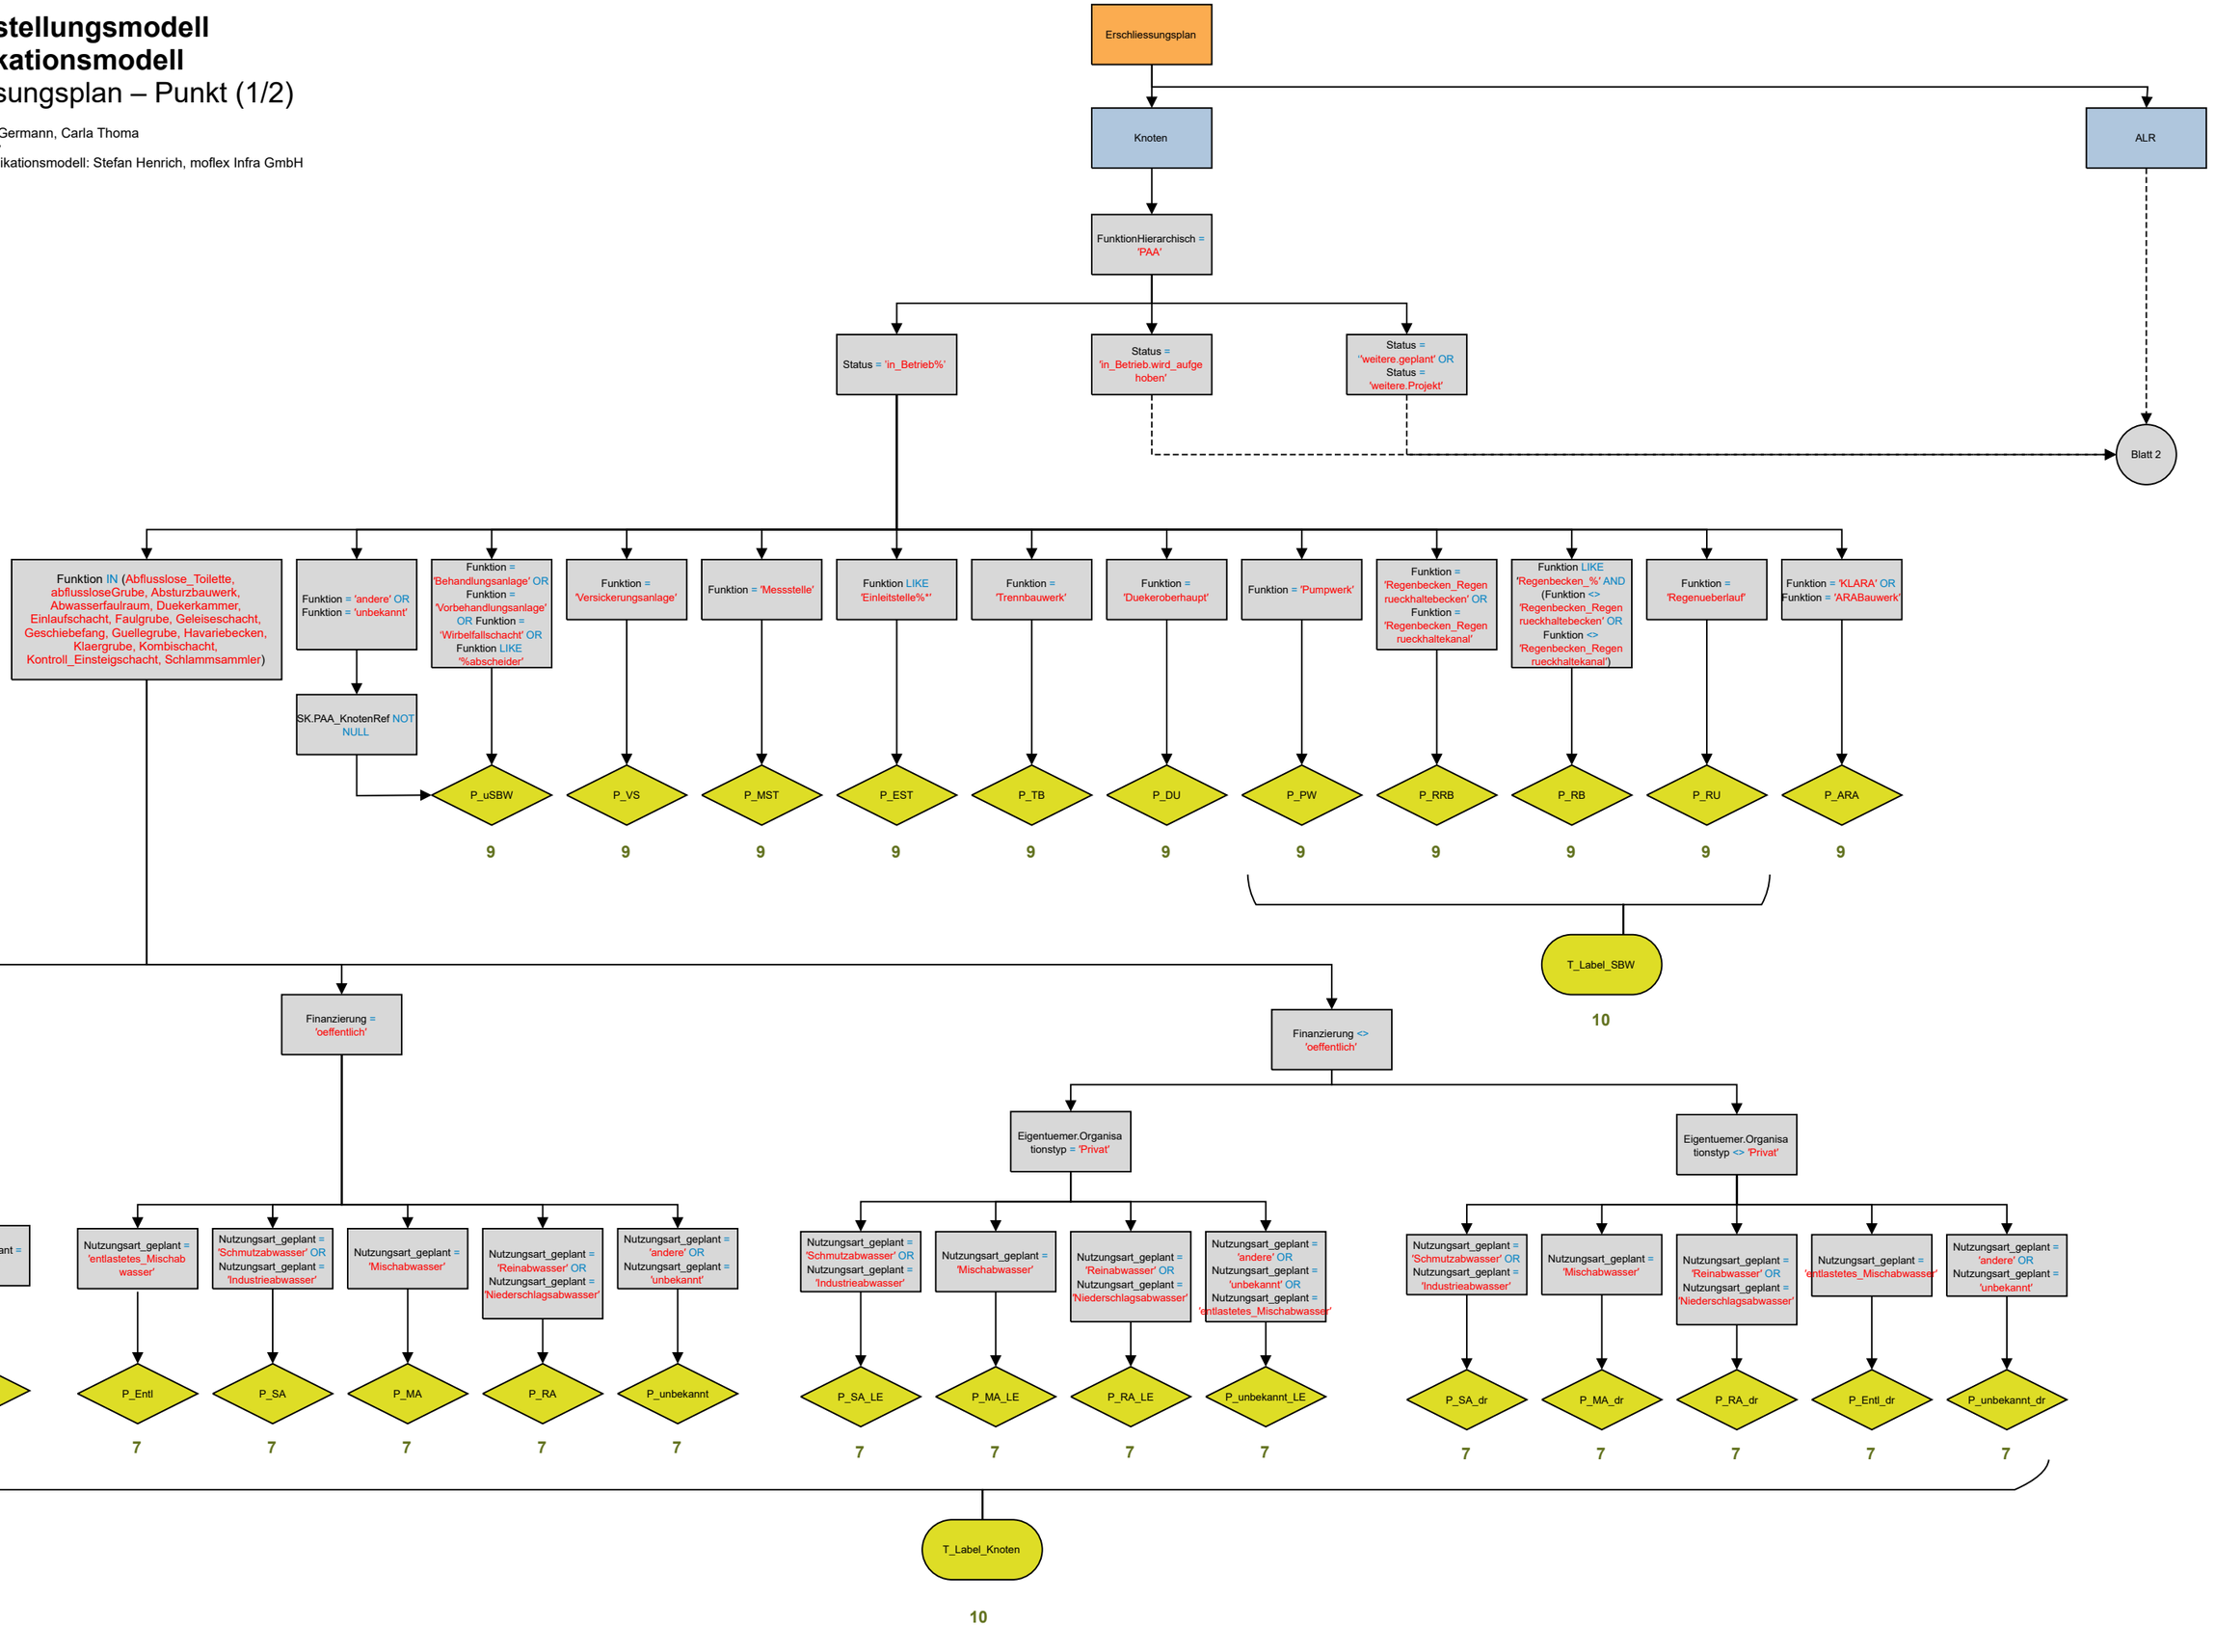

GEP Darstellungsmodell für Publikationsmodell

Erschliessungsplan – Punkt (2/2)

Bearbeitung: Judith Germann, Carla Thoma
Freigabe: Jürg Lüthy
Bearbeitung für Publikationsmodell: Stefan Henrich, moflex Infra GmbH
Version 0.8.3

